


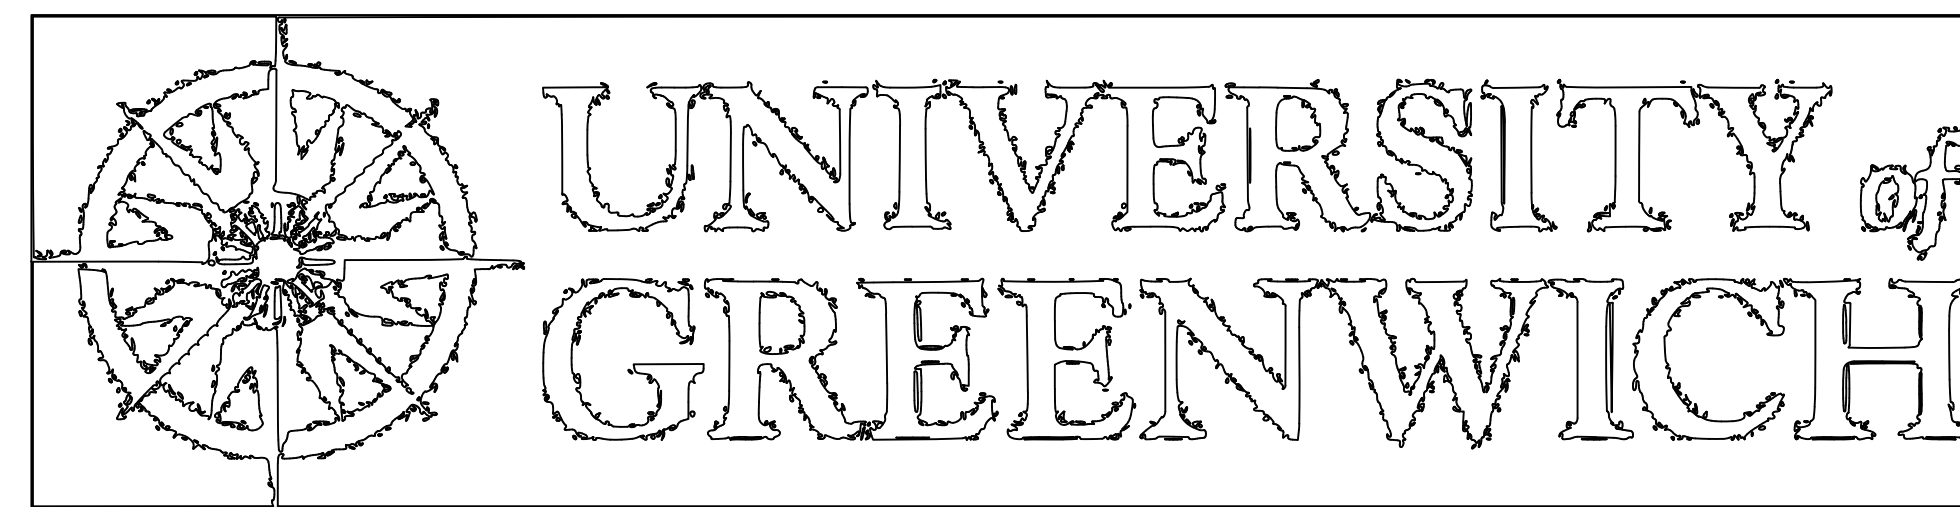

OCTOBER UNIVERSITY
FOR MODERN SCIENCE & ARTS
Architectural Engineering Department
2023

Architecture Department

ASE 552

Working Drawing 4

Project:

Mall Building

Name: Abdullah Refat
ID: 195267 Group: C

Instructors:
Dr. Tarek Galal

A0

Type:-	No.	Drawing Name
Architectural	A 0	Cover Sheet A0
Architectural	A 1	Drawing List A-01
Architectural	A 2	Ground floor plan A-02
Architectural	A 3	Mezannine floor plan A-03
Architectural	A 4	Typical floor plan A-04
Architectural	A 5	Basement 1 Floor Plan A-05
Architectural	A 6	Basement 2 Floor Plan A-06
Architectural	A 7	Roof Floor Plan A-07
Architectural	A 8	Site Plan A-08
Architectural	A 9	Sec A-A, A-09
Architectural	A10	West Elevation A-10
Architectural	A 2	Ground 1 floor plan A-11
Architectural	A 2	Ground 2 floor plan A-12
Architectural	A 2	Elevation 1 floor plan A-13
Architectural	A 2	Section 1 floor plan A-14
Architectural	A 10	Stair Details A-15
Architectural	A 11	Working Details A-16
Architectural	A 12	Working stair Details A-17
Architectural	A 17	Working elevator Details A-18
Architectural	A 18	Working Details A-19
Architectural	A 19	Working Details A-20
Architectural	A 20	Insulation Details A-21
Architectural	A 21	Wall section Details A-22
Architectural	A 22	Wall section Details A-23

Plain concrete	Plain concrete	
Plain concrete	Symbols	Name
Reinforced concrete	D	Doors
Brick Wall	W	Windows
Mortar	SEC. No Sheet No.	Section
Sand	Detail. No Sheet No.	Wall section
Thermal insulation	Elev. No Sheet No.	Elevation
Moisture insulation	N Sheet N	Callouts
		Stair direction
	+0.00 M	Top of slab level
	+0.00 M	Finish floor level

Abdullah refat	Course Name: Working Drawing 4	Mall Building	A-01	Msa University Facualty of Engineering Architecture Department	
ID:195267	Course Code: ASE 552				Drawing List
	Group: C				



OCTOBER UNIVERSITY
FOR MODERN SCIENCES & ARTS
Architectural Engineering Department
Fall 2022

A-01



OCTOBER UNIVERSITY
FOR MODERN SCIENCES & ARTS
Architectural Engineering Department
Fall 2022

Faculty Info

Instructors:
Dr. Tarek Galal

Assistant:
Eng.

Assignment No. :

Ground floor plan
Scale 1:100


Date: / / 2023

Week Number:

Student Name: Abdullah refat

ID: 195267

A-02

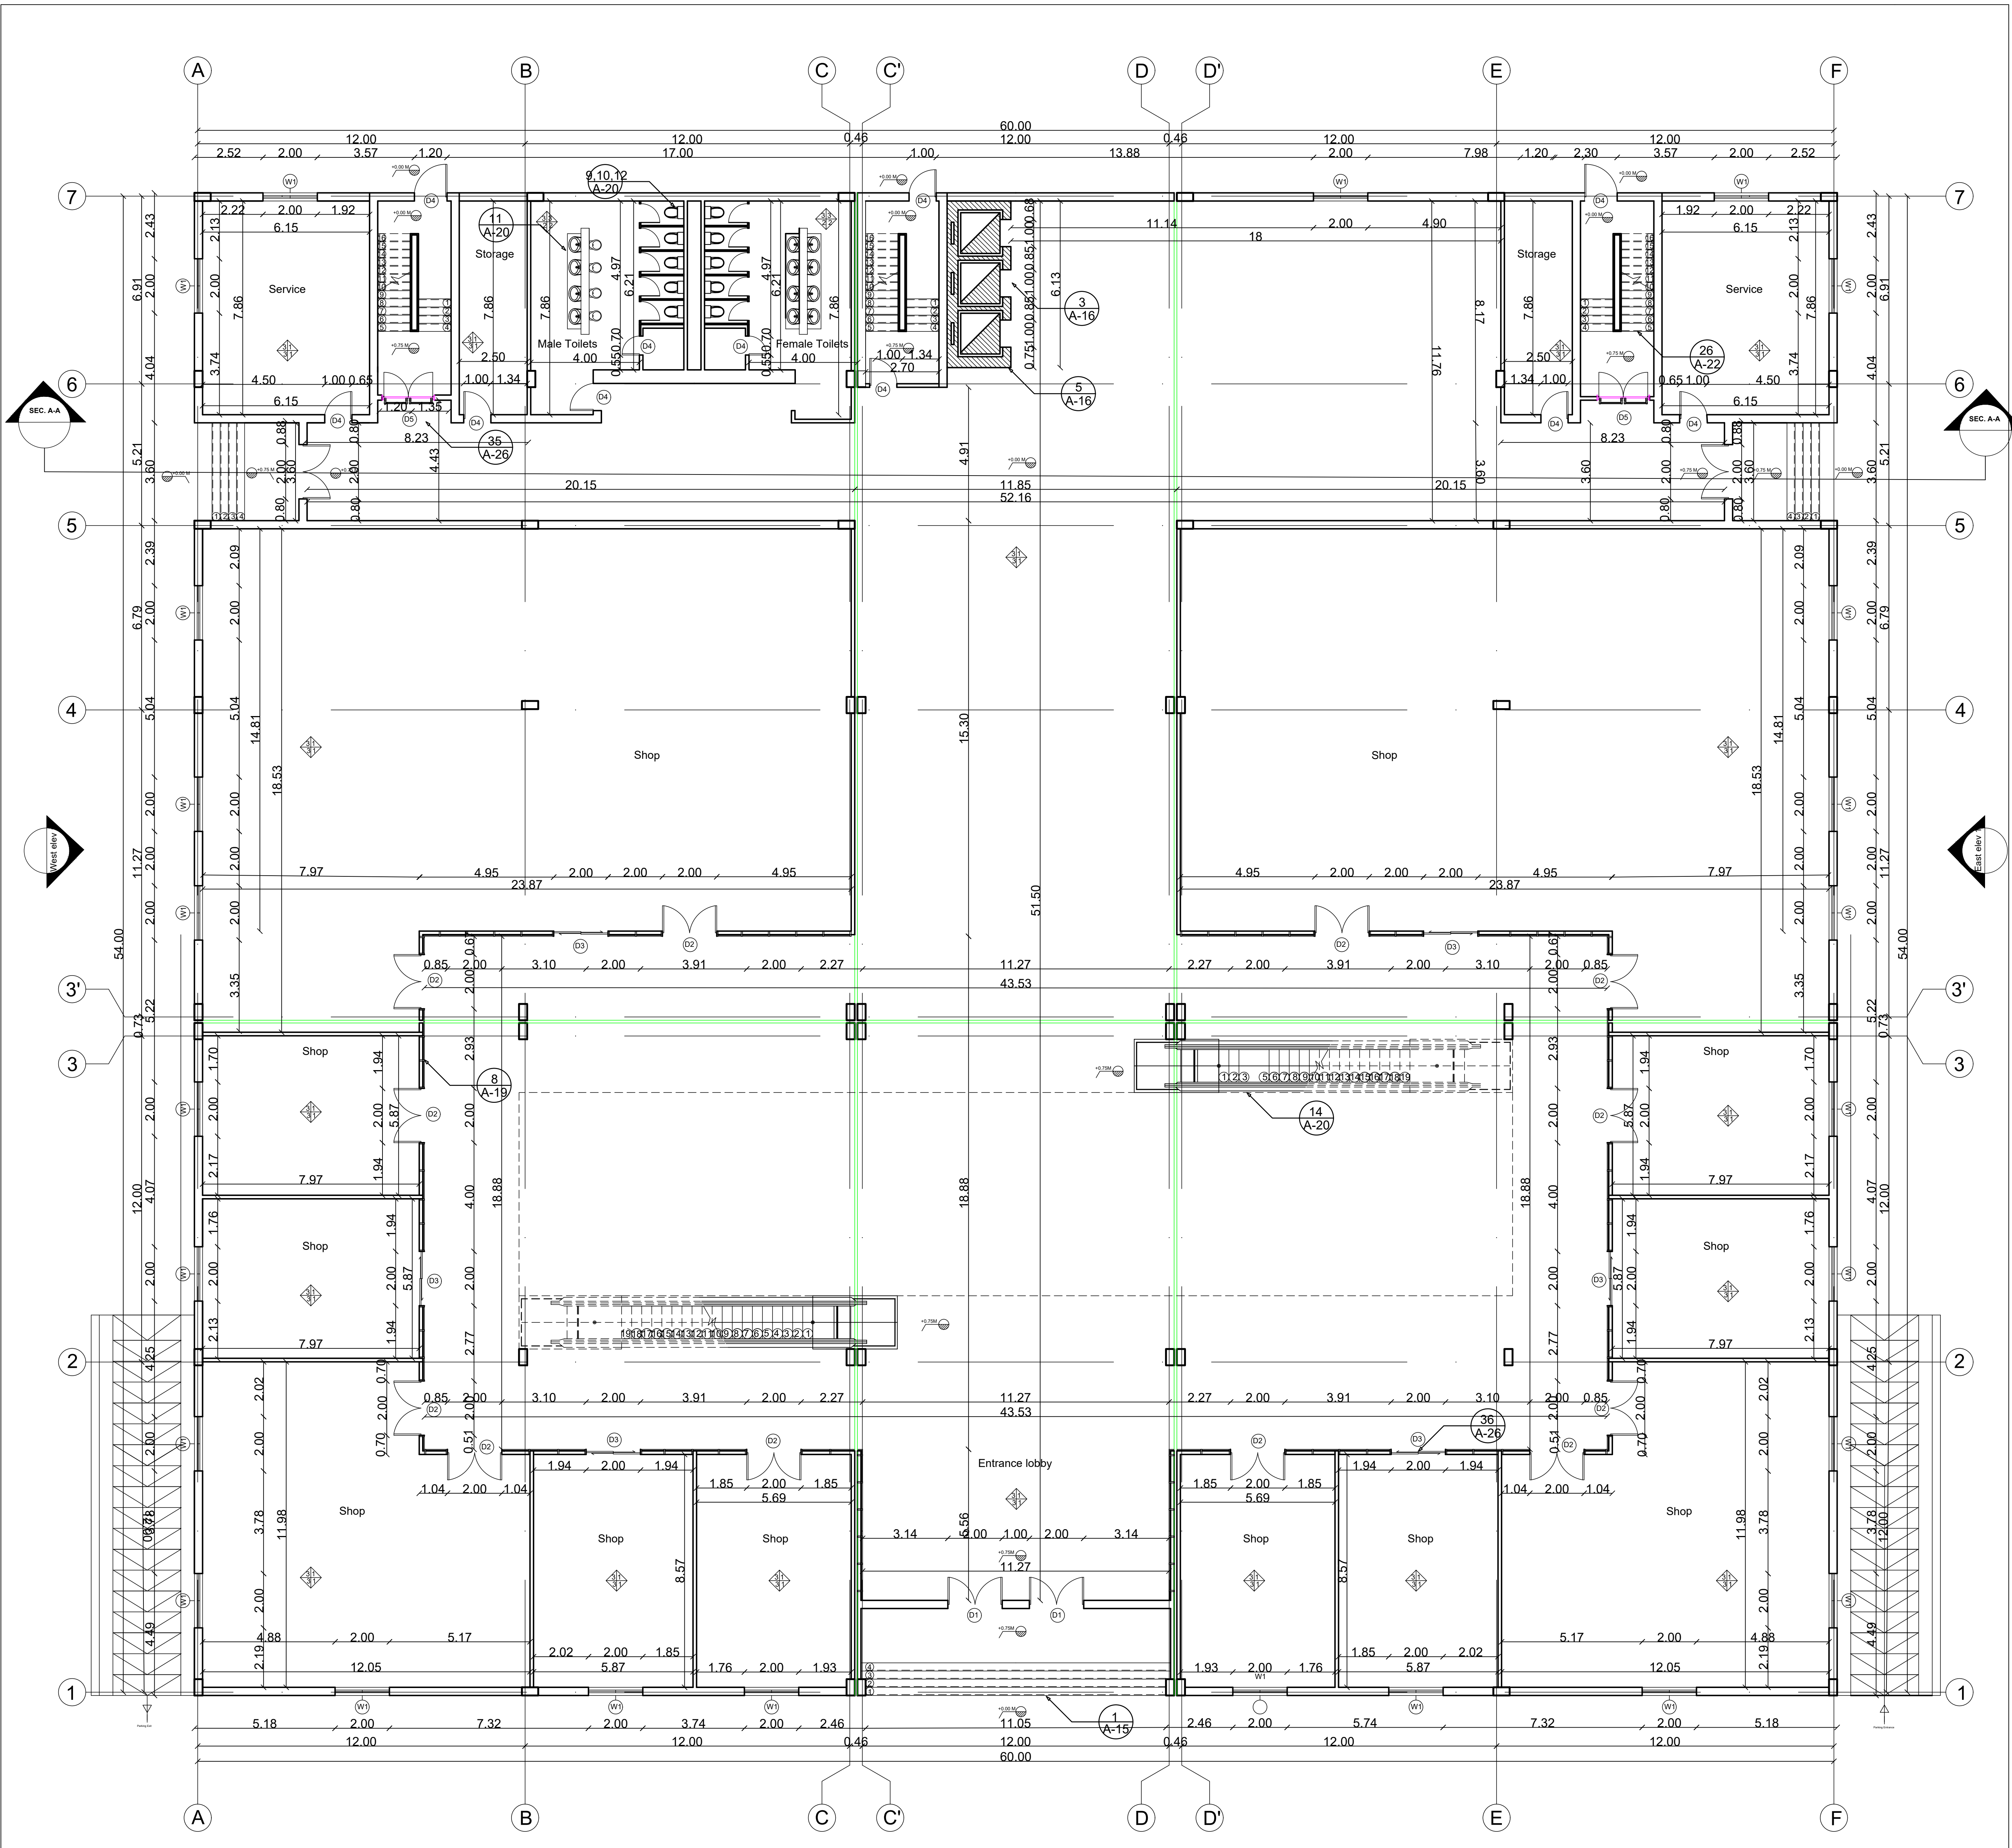

Window types		
name	width	Material
W1	0.5 M	Aluminum frame ,Hooper
W2	1.0 M	Aluminum frame ,sliding
W3	2.0 M	Aluminum frame ,sliding
W4	0.5 M	Aluminum frame ,Awning

Door types		
name	width	Material
D1	2.00 M	Glass Hinged door,2leaf
D2	2.00 M	Glass acoustic door,2leaf
D3	2.00 M	Glass Sliding door,2leaf
D4	1.00 M	Wooden hinged door,1leaf
D5	2.00 M	Panic bar Aluminum Sliding door,2leaf

Finishing materials		
Type	No.	Description
Ceiling	1	Plaster Gypsum
	2	False ceiling tiles
	3	Paint
Walls	1	Fiberglass board 25mm,(1")thick
	2	Ceramic tiles 60x60x0.8cm
	3	Paint
	4	Wood panels,tounge and grove decking
Skirting	1	wooden skirting
	2	Ceramic tiles 60x60x0.8cm
	3	Marble skirting
Flooring	1	Paint
	2	Carpet
	3	Ceramic tiles 60x60x0.8cm
	4	Vinyl tiles



OCTOBER UNIVERSITY
FOR MODERN SCIENCES & ARTS
Architectural Engineering Department
Fall 2022

Faculty Info

Instructors:
Dr. Tarek Galal

Assistant:
Eng.

Assignment No. :

Mezzanine floor
plan Scale 1:100


Date: / / 2023

Week Number:

Student Name: Abdullah refat

ID: 195267


A-03

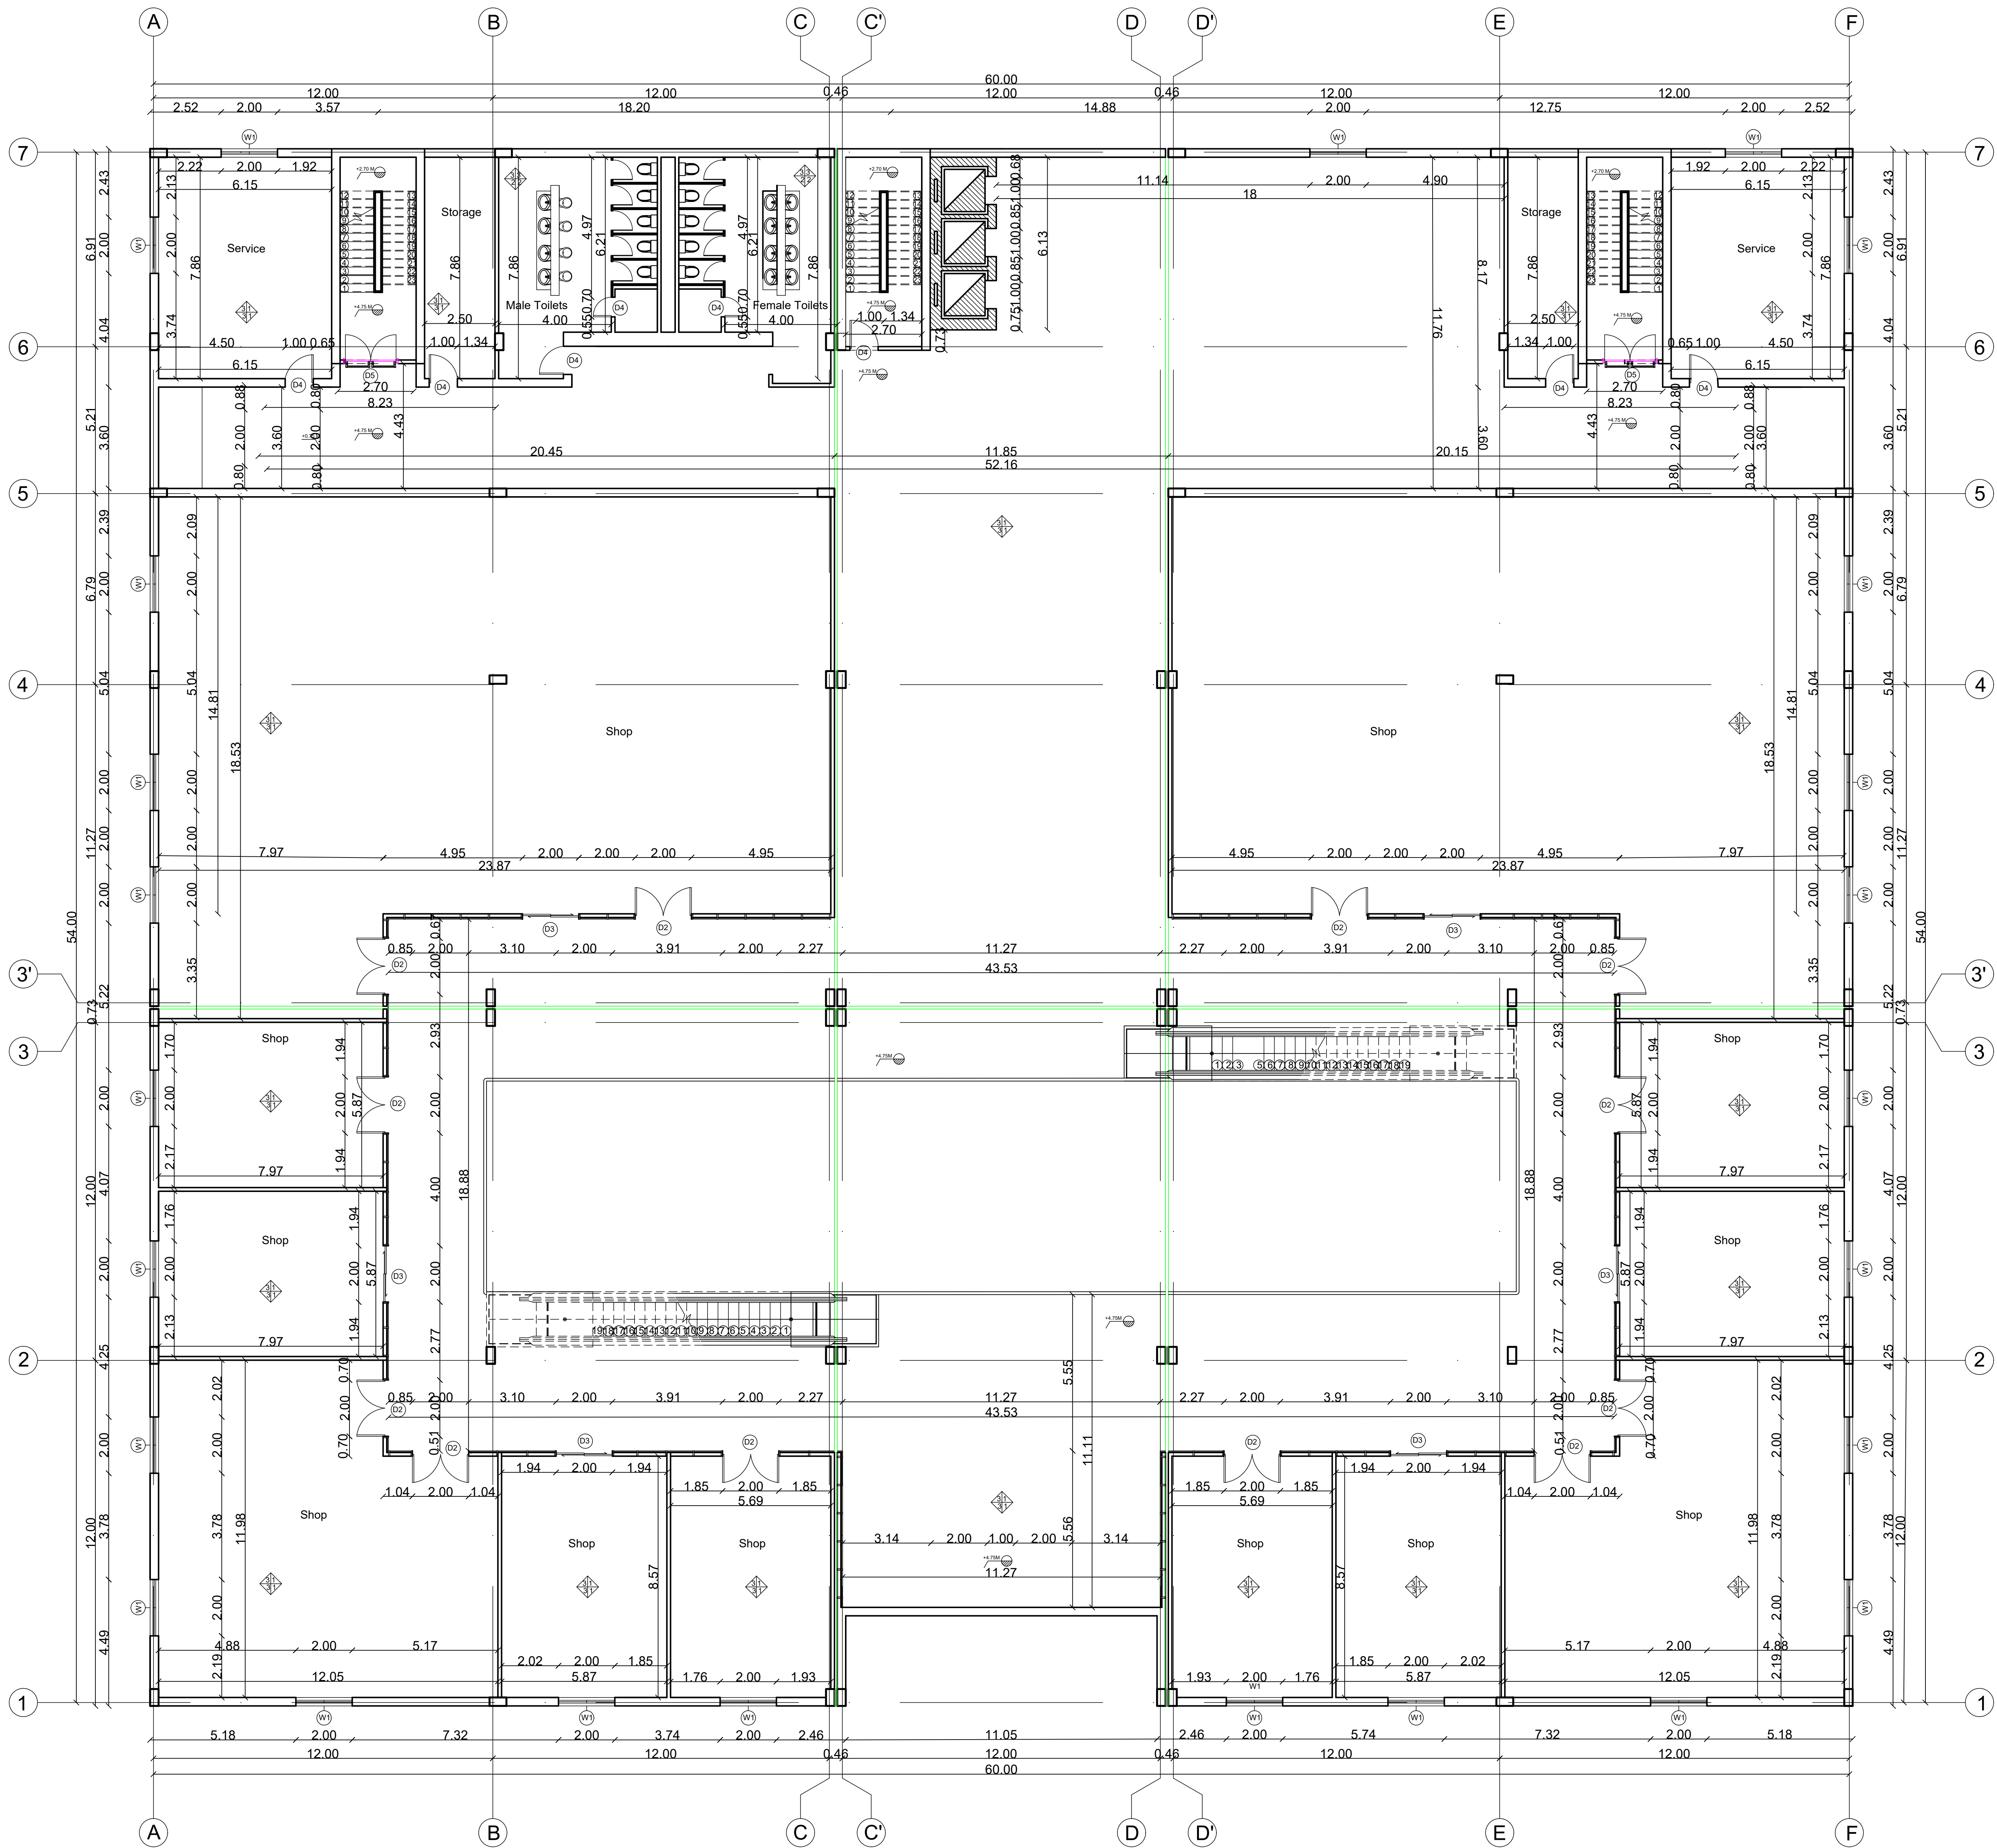

Window types		
name	width	Material
W1	0.5 M	Aluminum frame ,Hooper
W2	1.0 M	Aluminum frame ,sliding
W3	2.0 M	Aluminum frame ,sliding
W4	0.5 M	Aluminum frame ,Awning

Door types		
name	width	Material
D1	2.00 M	Glass Hinged door,2leaf
D2	2.00 M	Glass acoustic door,2leaf
D3	2.00 M	Glass Sliding door,2leaf
D4	1.00 M	Wooden hinged door,1leaf
2.00 M		Panic bar Aluminum Sliding door,2leaf

Finishing materials		
Type	No.	Description
Ceiling	1	Plaster Gypsum
	2	False ceiling tiles
	3	Paint
Walls	1	Fiberglass board 25mm,(1")thick
	2	Ceramic tiles 60x60x0.8cm
	3	Paint
	4	Wood panels,tounge and grove decking
Skirting	1	wooden skirting
	2	Ceramic tiles 60x60x0.8cm
	3	Marble skirting
Flooring	1	Paint
	2	Carpet
	3	Ceramic tiles 60x60x0.8cm
	4	Vinyl tiles

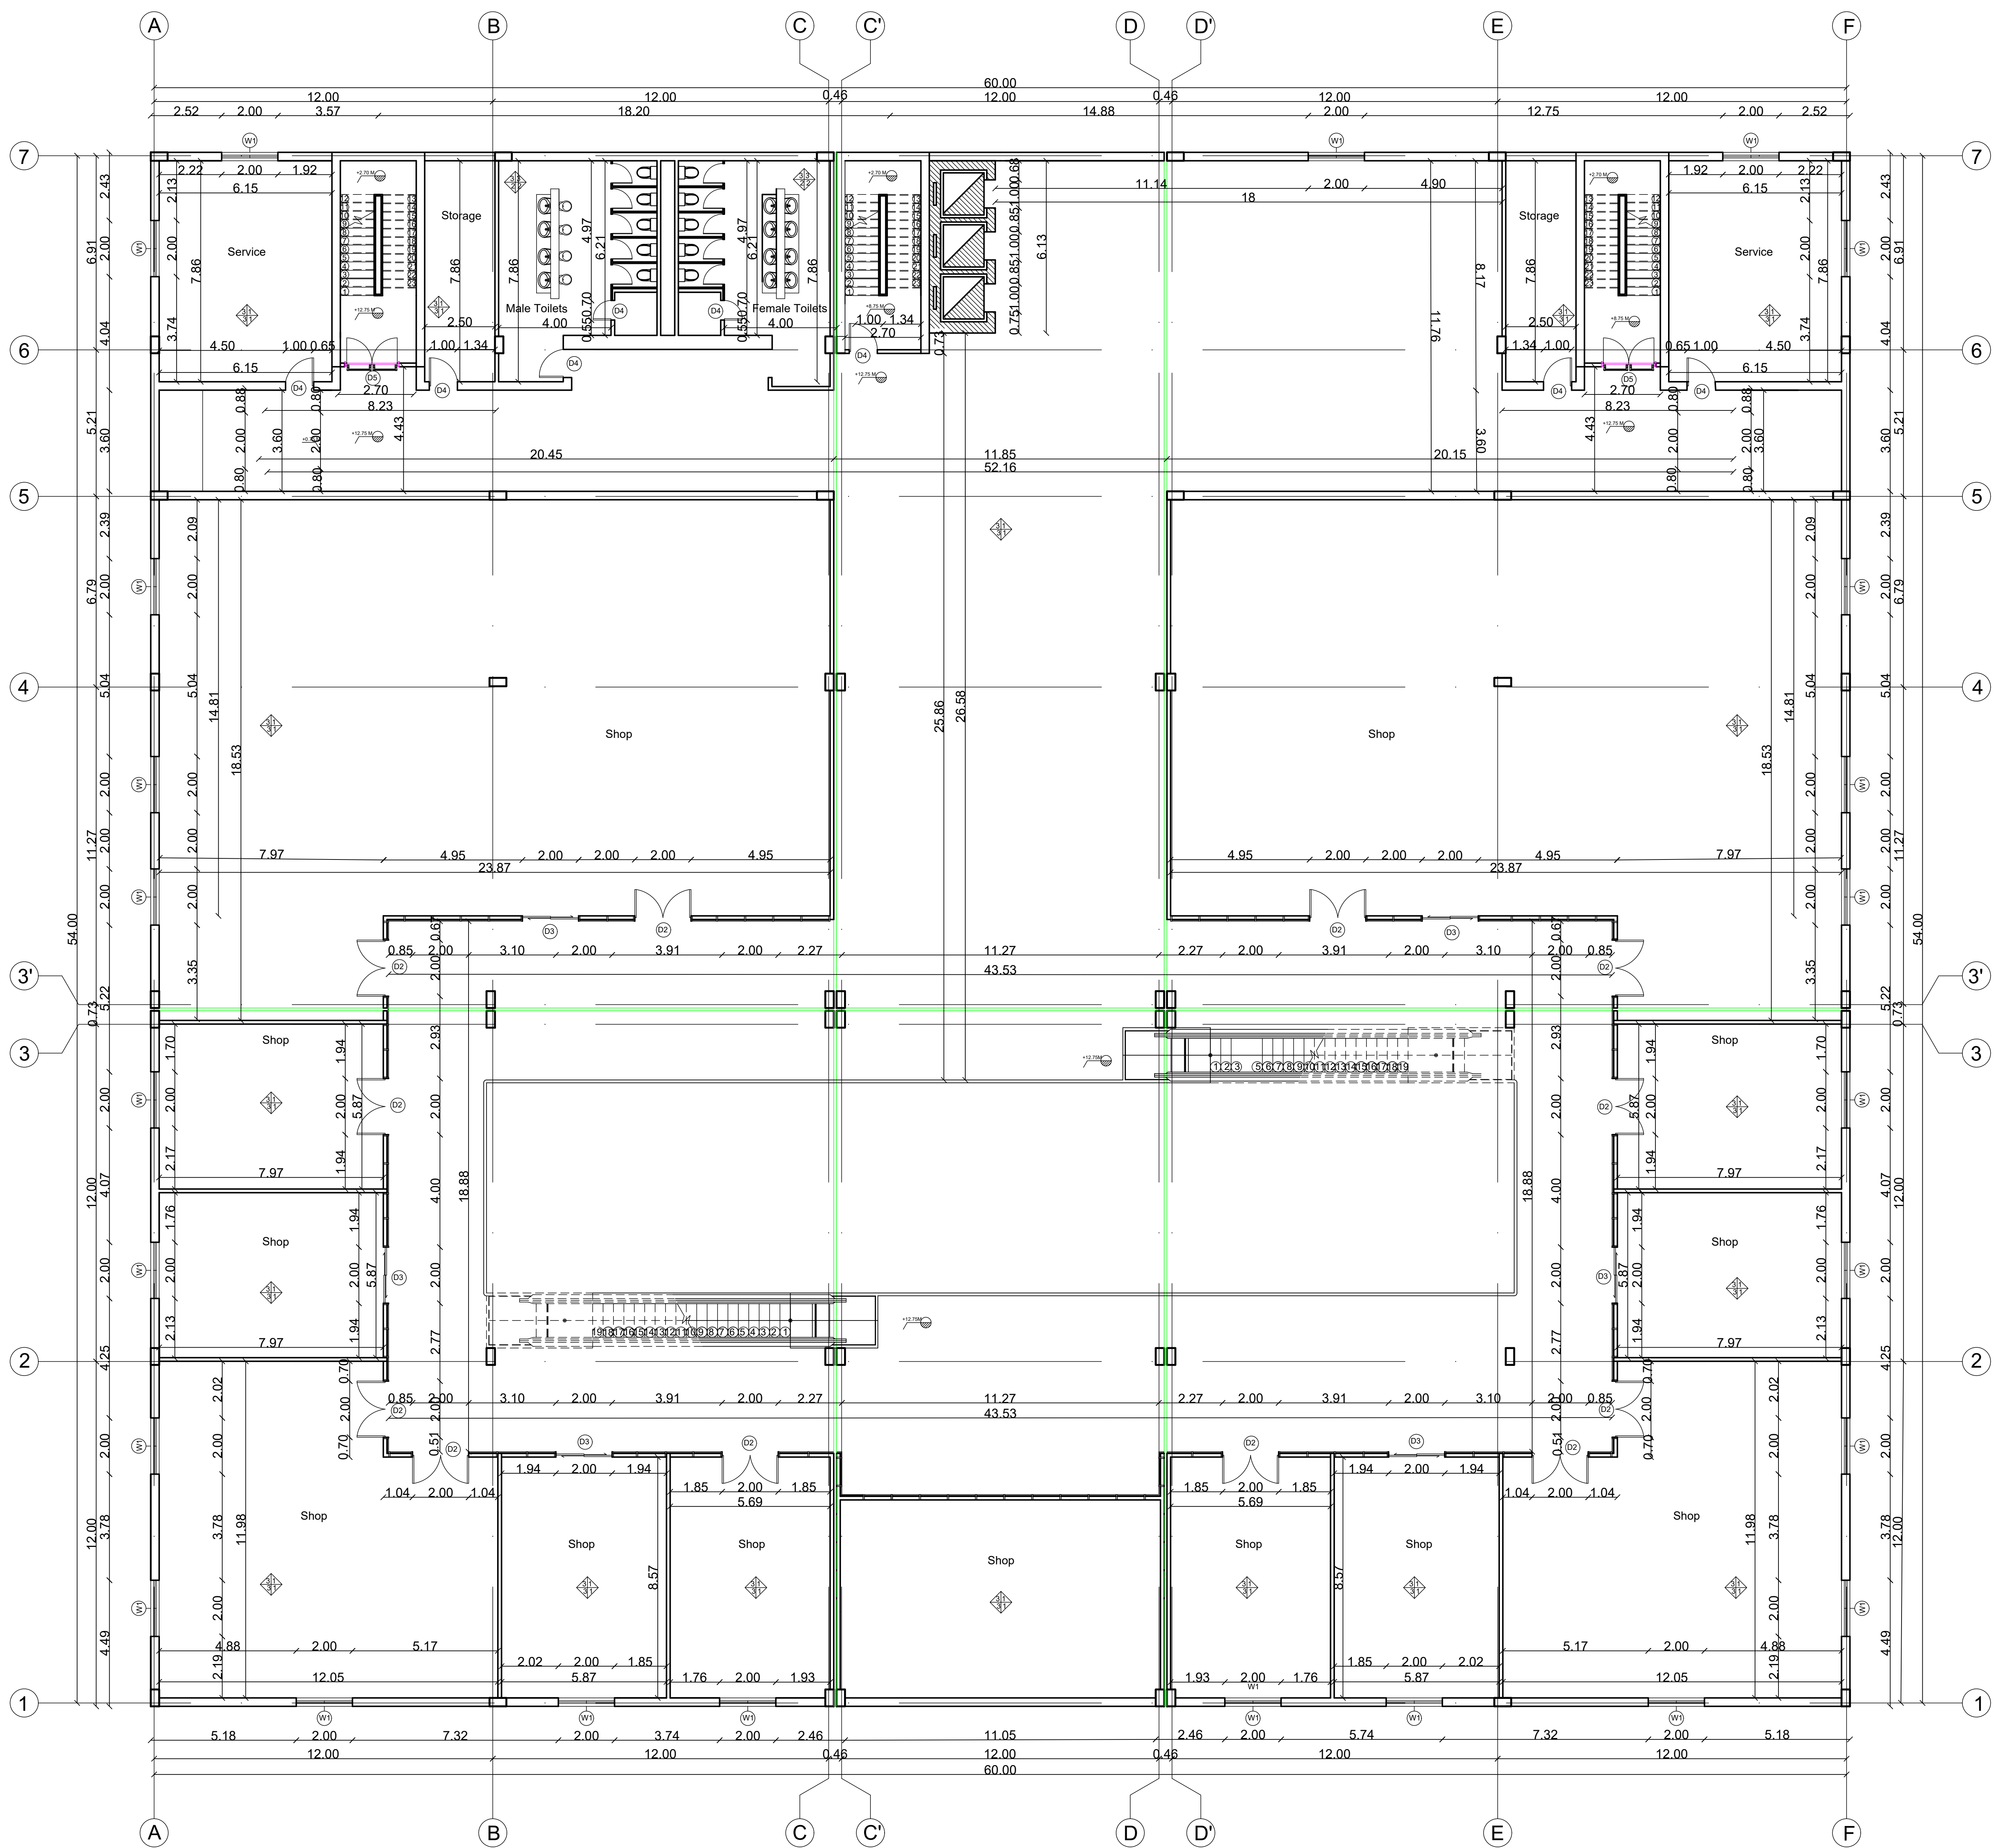

Window types		
name	width	Material
W1	0.5 M	Aluminum frame ,Hooper
W2	1.0 M	Aluminum frame ,sliding
W3	2.0 M	Aluminum frame ,sliding
W4	0.5 M	Aluminum frame ,Awning

Door types		
name	width	Material
D1	2.00 M	Glass Hinged door,2leaf
D2	2.00 M	Glass acoustic door,2leaf
D3	2.00 M	Glass Sliding door,2leaf
D4	1.00 M	Wooden hinged door,1leaf
D5	2.00 M	Panic bar Aluminum Sliding door,2leaf

Finishing materials		
Type	No.	Description
Ceiling	1	Plaster Gypsum
	2	False ceiling tiles
	3	Paint
Walls	1	Fiberglass board 25mm,(1")thick
	2	Ceramic tiles 60x60x0.8cm
	3	Paint
	4	Wood panels,tounge and grove decking
Skirting	1	wooden skirting
	2	Ceramic tiles 60x60x0.8cm
	3	Marble skirting
Flooring	1	Paint
	2	Carpet
	3	Ceramic tiles 60x60x0.8cm
	4	Vinyl tiles



OCTOBER UNIVERSITY
FOR MODERN SCIENCES & ARTS
Architectural Engineering Department
Fall 2022

Faculty Info

Instructors:
Dr. Tarek Galal

Assistant:
Eng.

Assignment No. :

Typical floor plan Scale 1:100

Date: / / 2023

Week Number:

Student Name: Abdullah refat

ID: 195267

A-04



OCTOBER UNIVERSITY
FOR MODERN SCIENCES & ARTS
Architectural Engineering Department
Fall 2022

Faculty Info

Instructors:
Dr. Tarek Galal

Assistant:
Eng.

Assignment No. :

Basement 1 floor plan Scale 1:100


Date: / / 2023

Week Number:

Student Name: Abdullah refat

ID: 195267

A-05

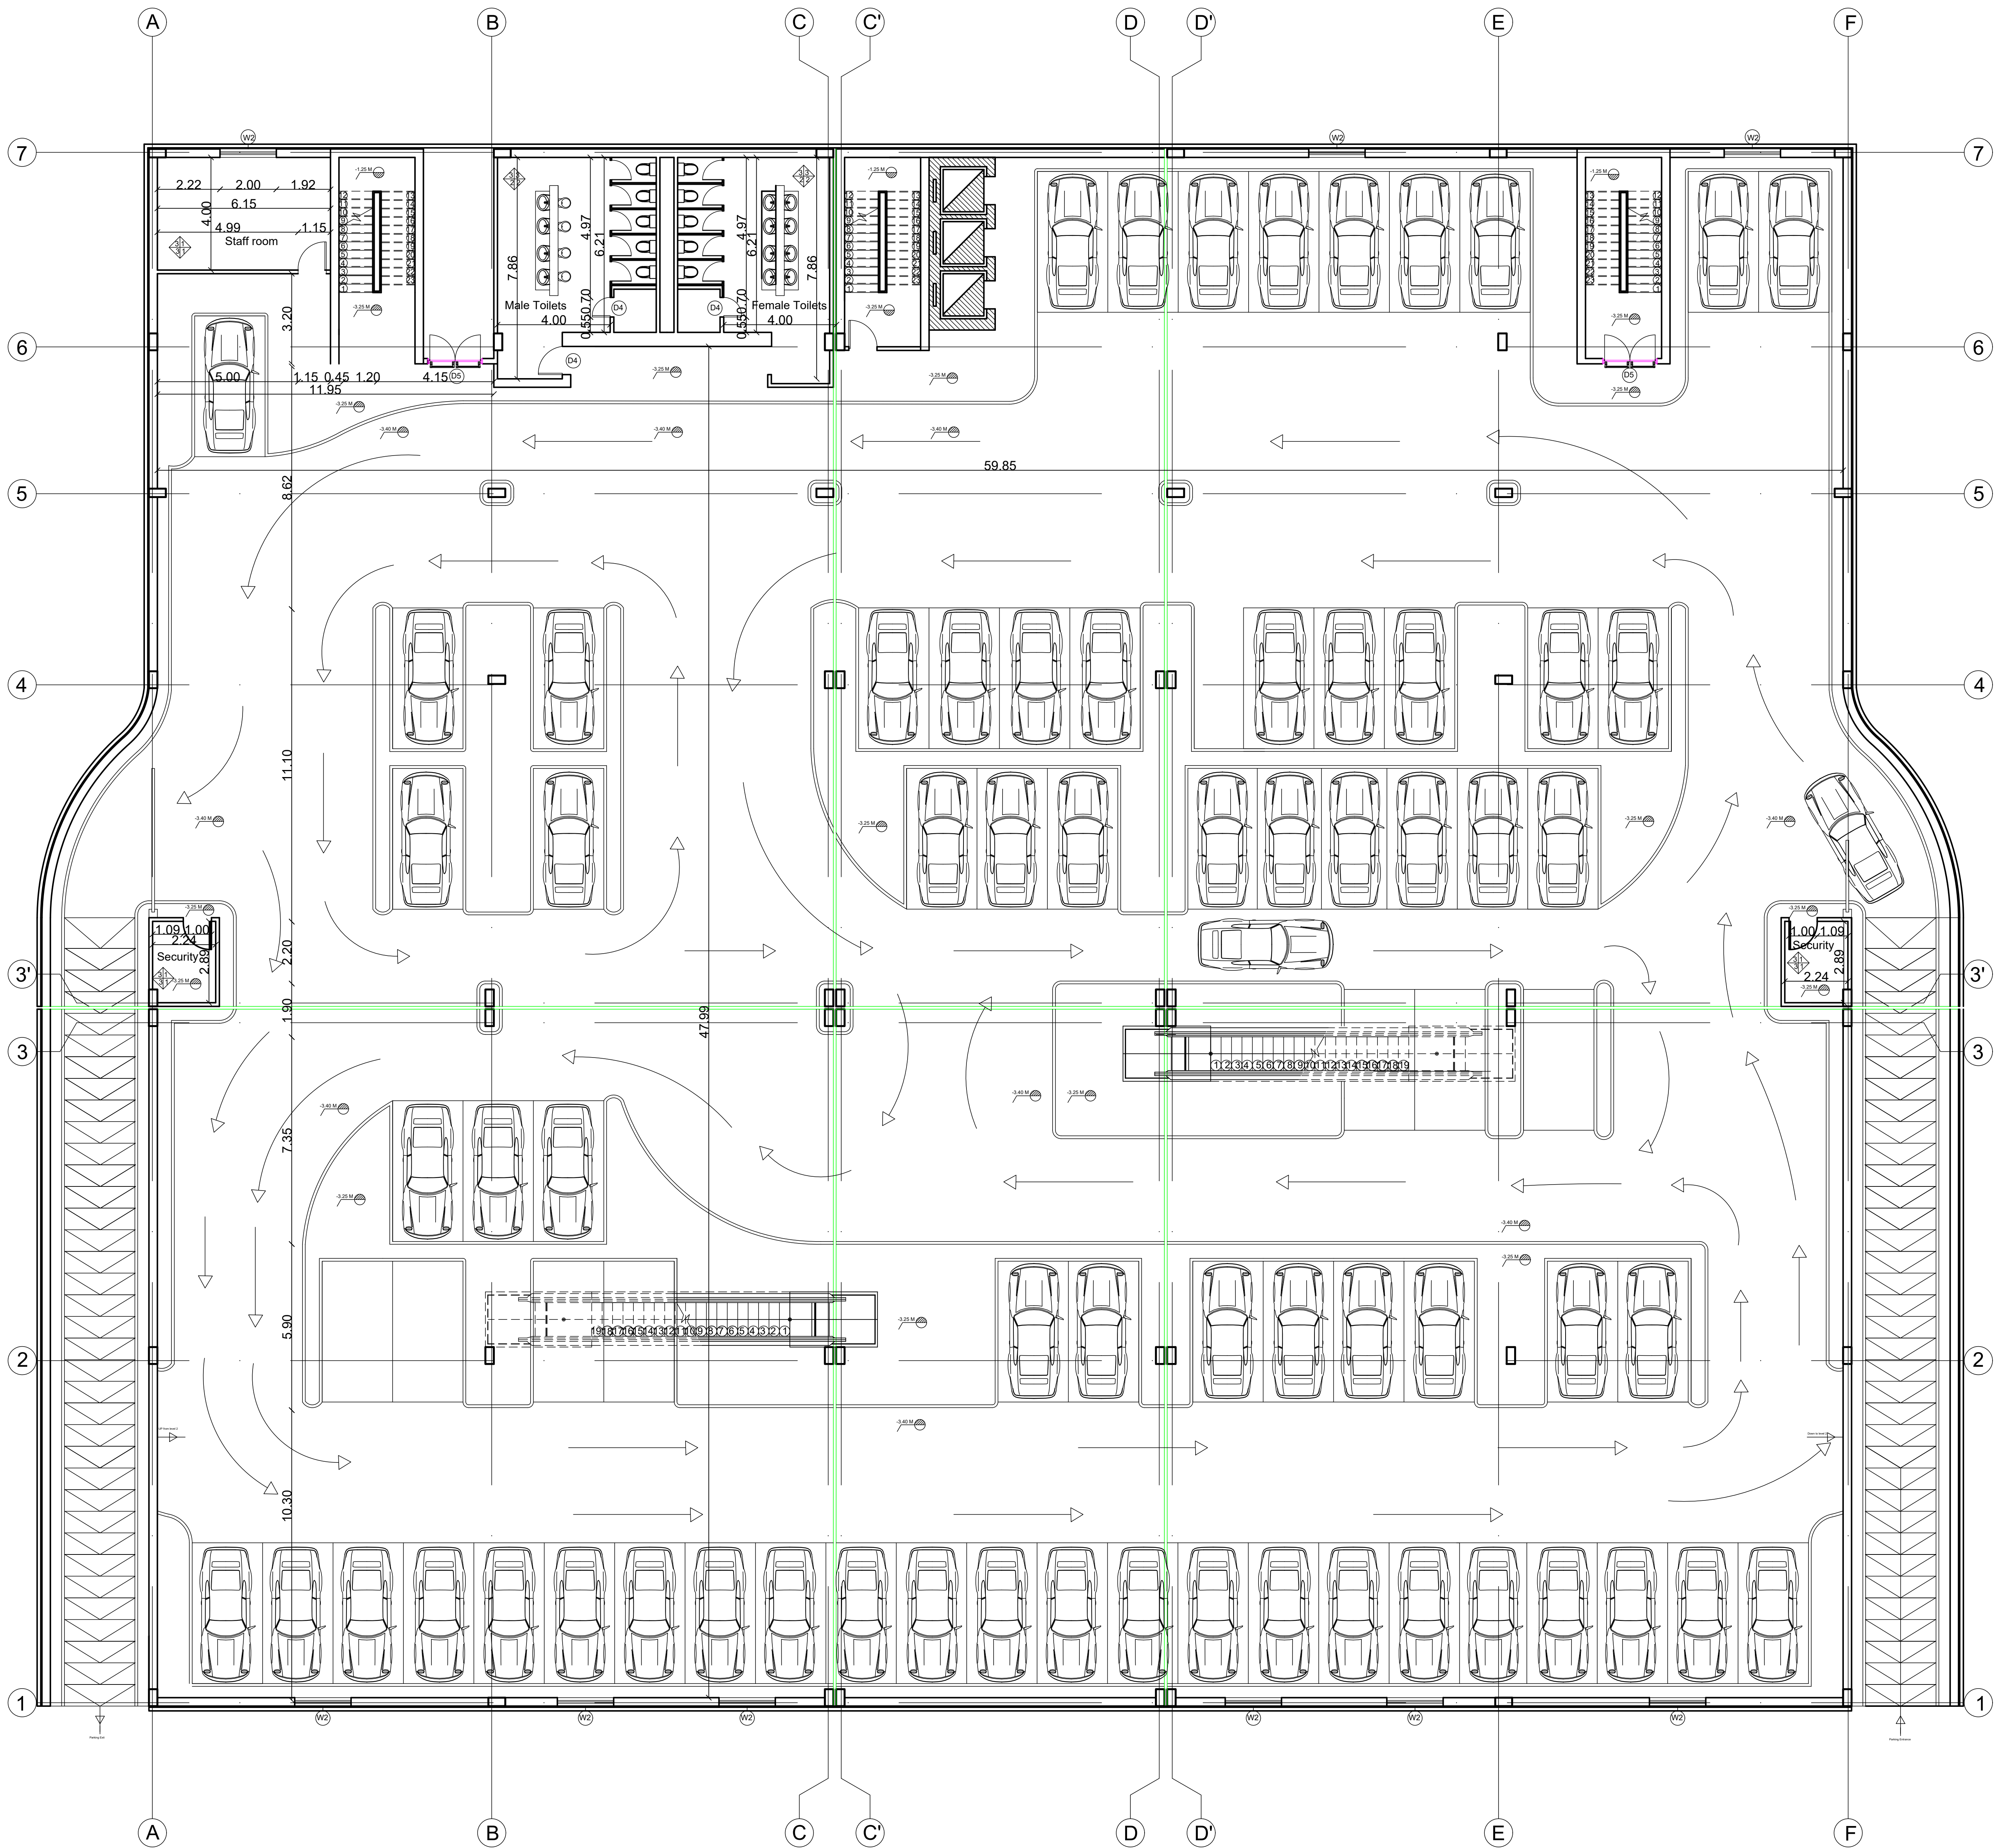

Window types		
name	width	Material
W1	0.5 M	Aluminum frame ,Hooper
W2	1.0 M	Aluminum frame ,sliding
W3	2.0 M	Aluminum frame ,sliding
W4	0.5 M	Aluminum frame ,Awning

Door types		
name	width	Material
D1	2.00 M	Glass Hinged door,2leaf
D2	2.00 M	Glass acoustic door,2leaf
D3	2.00 M	Glass Sliding door,2leaf
D4	1.00 M	Wooden hinged door,1leaf
D5	2.00 M	Panic bar Aluminum Sliding door,2leaf

Finishing materials		
Type	No.	Description
Ceiling	1	Plaster Gypsum
	2	False ceiling tiles
	3	Paint
Walls	1	Fiberglass board ,25mm,(1"thick
	2	Ceramic tiles 60x60x0.8cm
	3	Paint
	4	Wood panels,lounge and grove decking
Skirting	1	wooden skirting
	2	Ceramic tiles 60x60x0.8cm
	3	Marble skirting
Flooring	1	Paint
	2	Carpet
	3	Ceramic tiles 60x60x0.8cm
	4	Vinyl tiles



OCTOBER UNIVERSITY
FOR MODERN SCIENCES & ARTS
Architectural Engineering Department
Fall 2022

Faculty Info

Instructors:
Dr. Tarek Galal

Assistant:
Eng.

Assignment No. :

Basement 2 floor plan Scale 1:100


Date: / / 2023

Week Number:

Student Name: Abdullah refat

ID: 195267


A-06

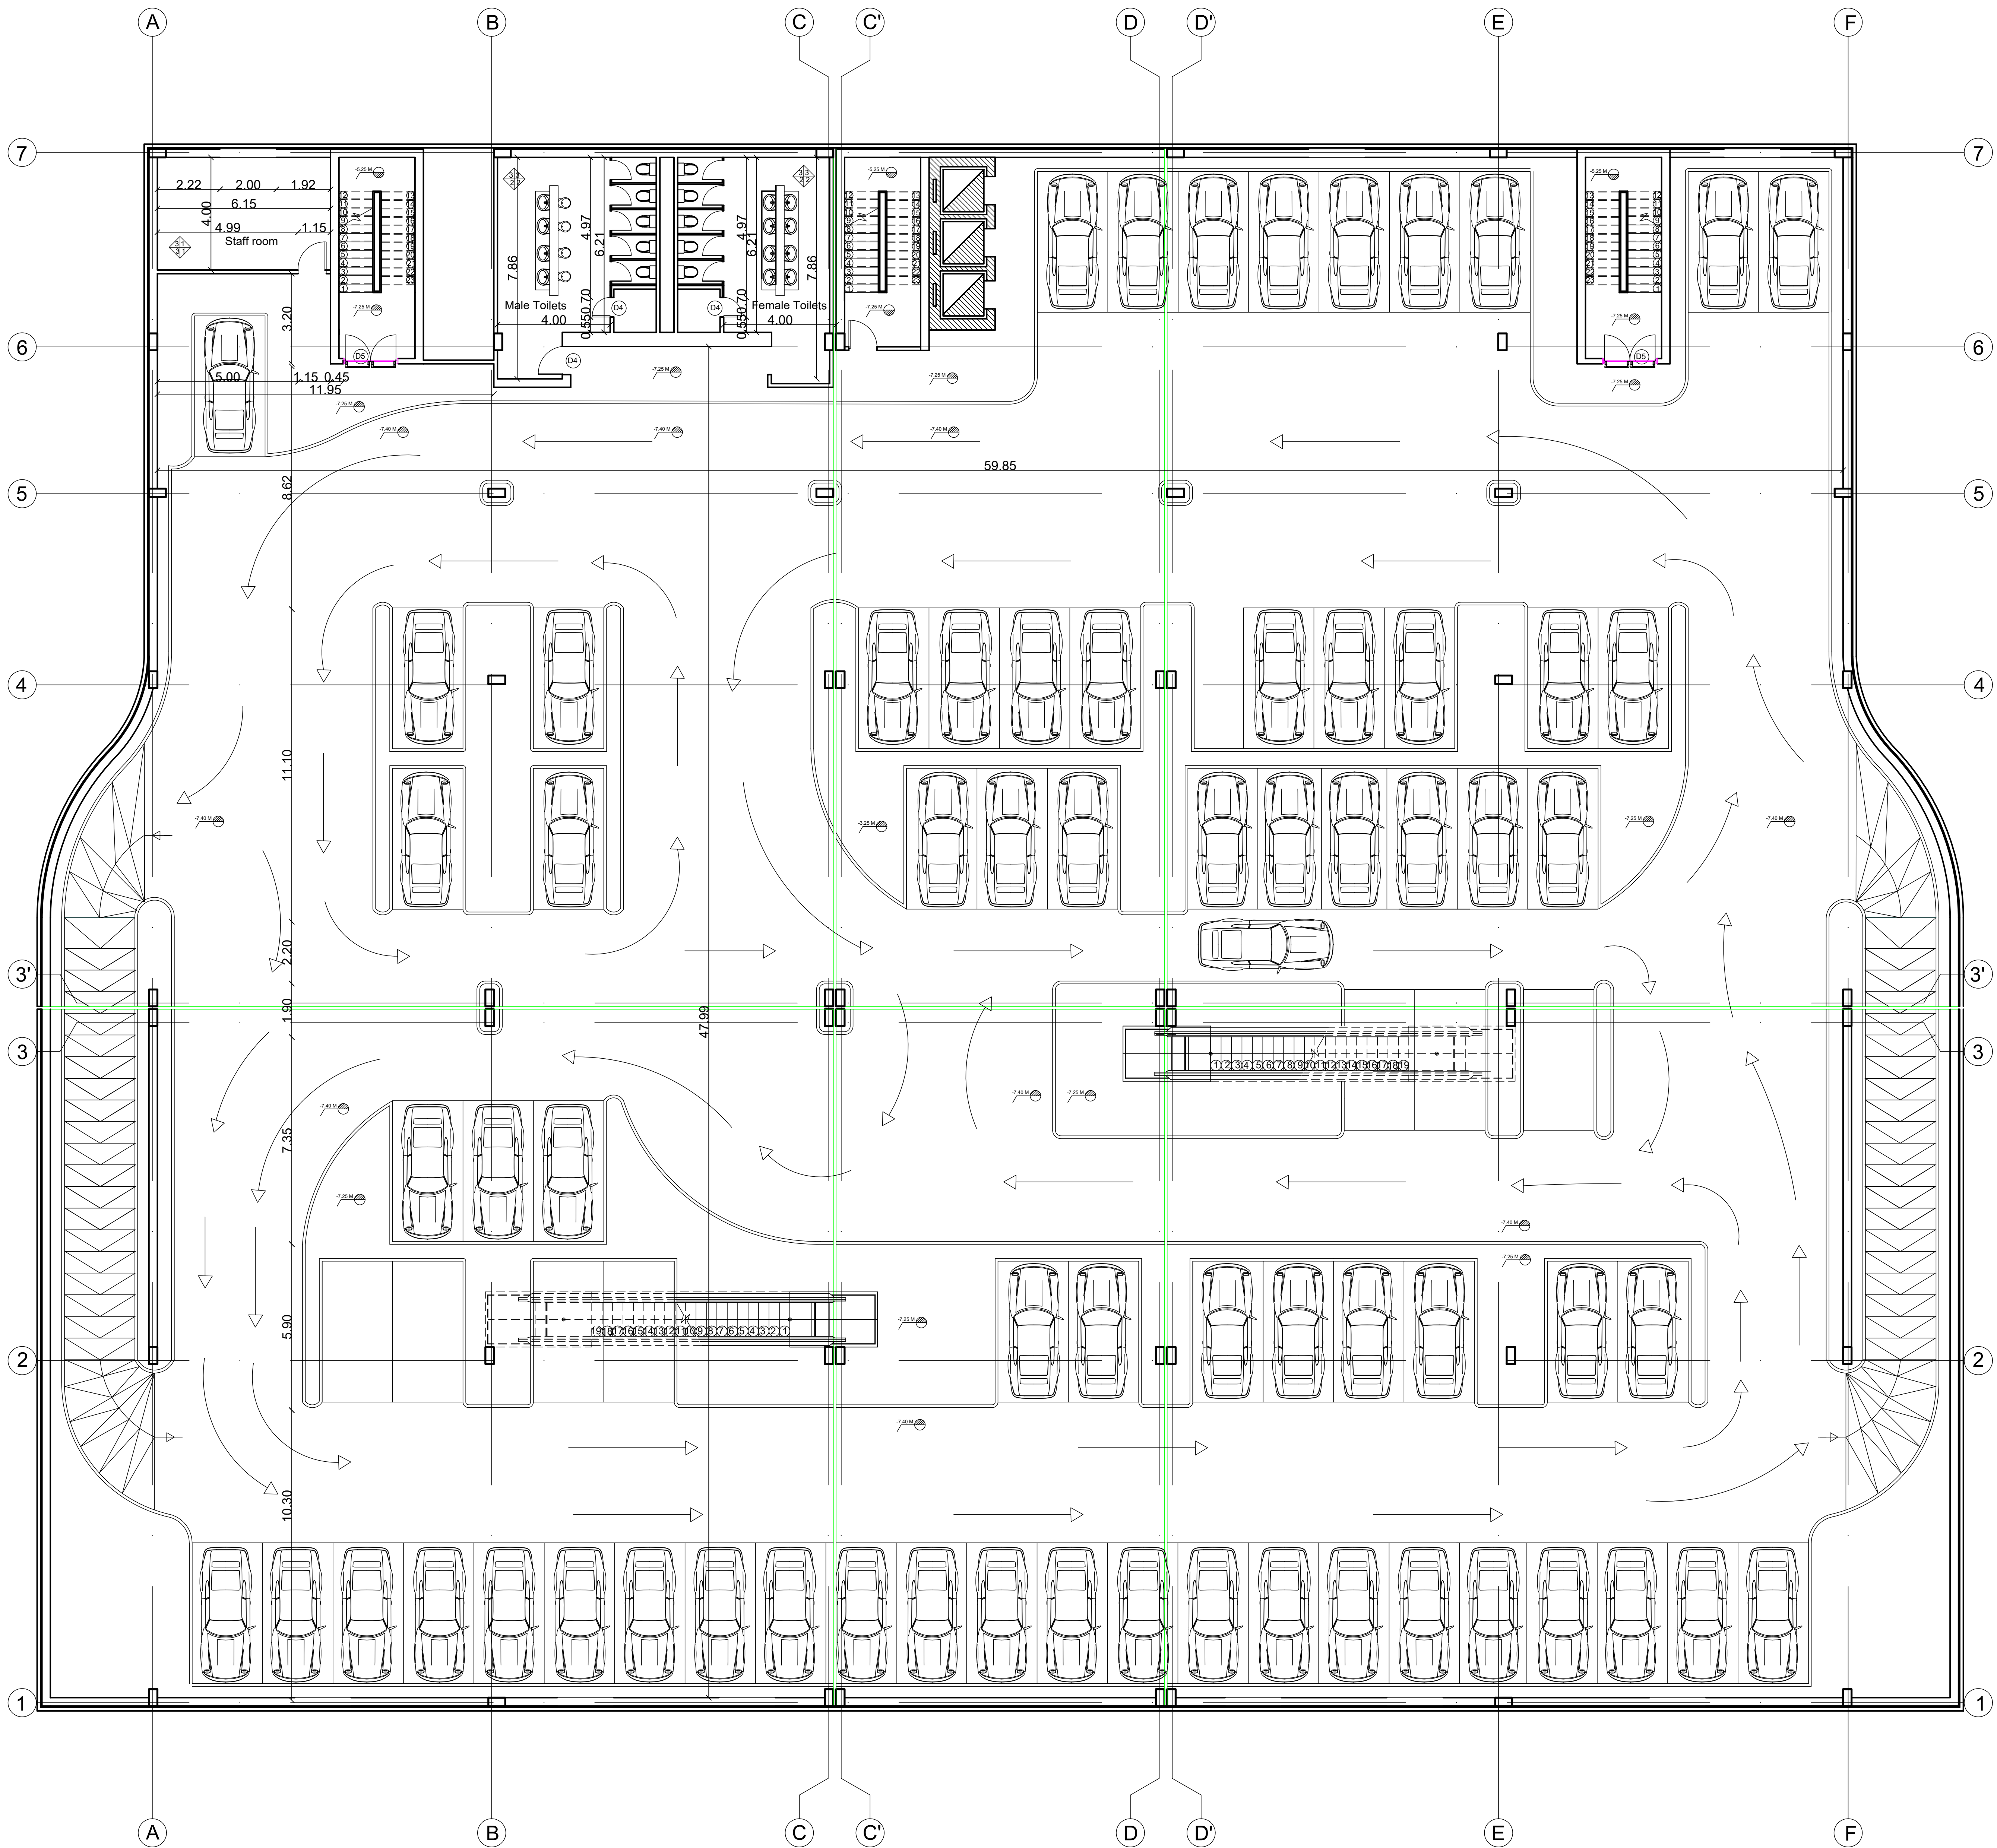

Window types		
name	width	Material
W1	0.5 M	Aluminum frame ,Hooper
W2	1.0 M	Aluminum frame ,sliding
W3	2.0 M	Aluminum frame ,sliding
W4	0.5 M	Aluminum frame ,Awning

Door types		
name	width	Material
D1	2.00 M	Glass Hinged door,2leaf
D2	2.00 M	Glass acoustic door,2leaf
D3	2.00 M	Glass Sliding door,2leaf
D4	1.00 M	Wooden hinged door,1leaf
D5	2.00 M	Panic bar Aluminum Sliding door,2leaf

Finishing materials		
Type	No.	Description
Ceiling	1	Plaster Gypsum
	2	False ceiling tiles
	3	Paint
Walls	1	Fiberglass board 25mm,(1"thick
	2	Ceramic tiles 60x60x0.8cm
	3	Paint
	4	Wood panels,lounge and grove decking
Skirting	1	wooden skirting
	2	Ceramic tiles 60x60x0.8cm
	3	Marble skirting
Flooring	1	Paint
	2	Carpet
	3	Ceramic tiles 60x60x0.8cm
	4	Vinyl tiles

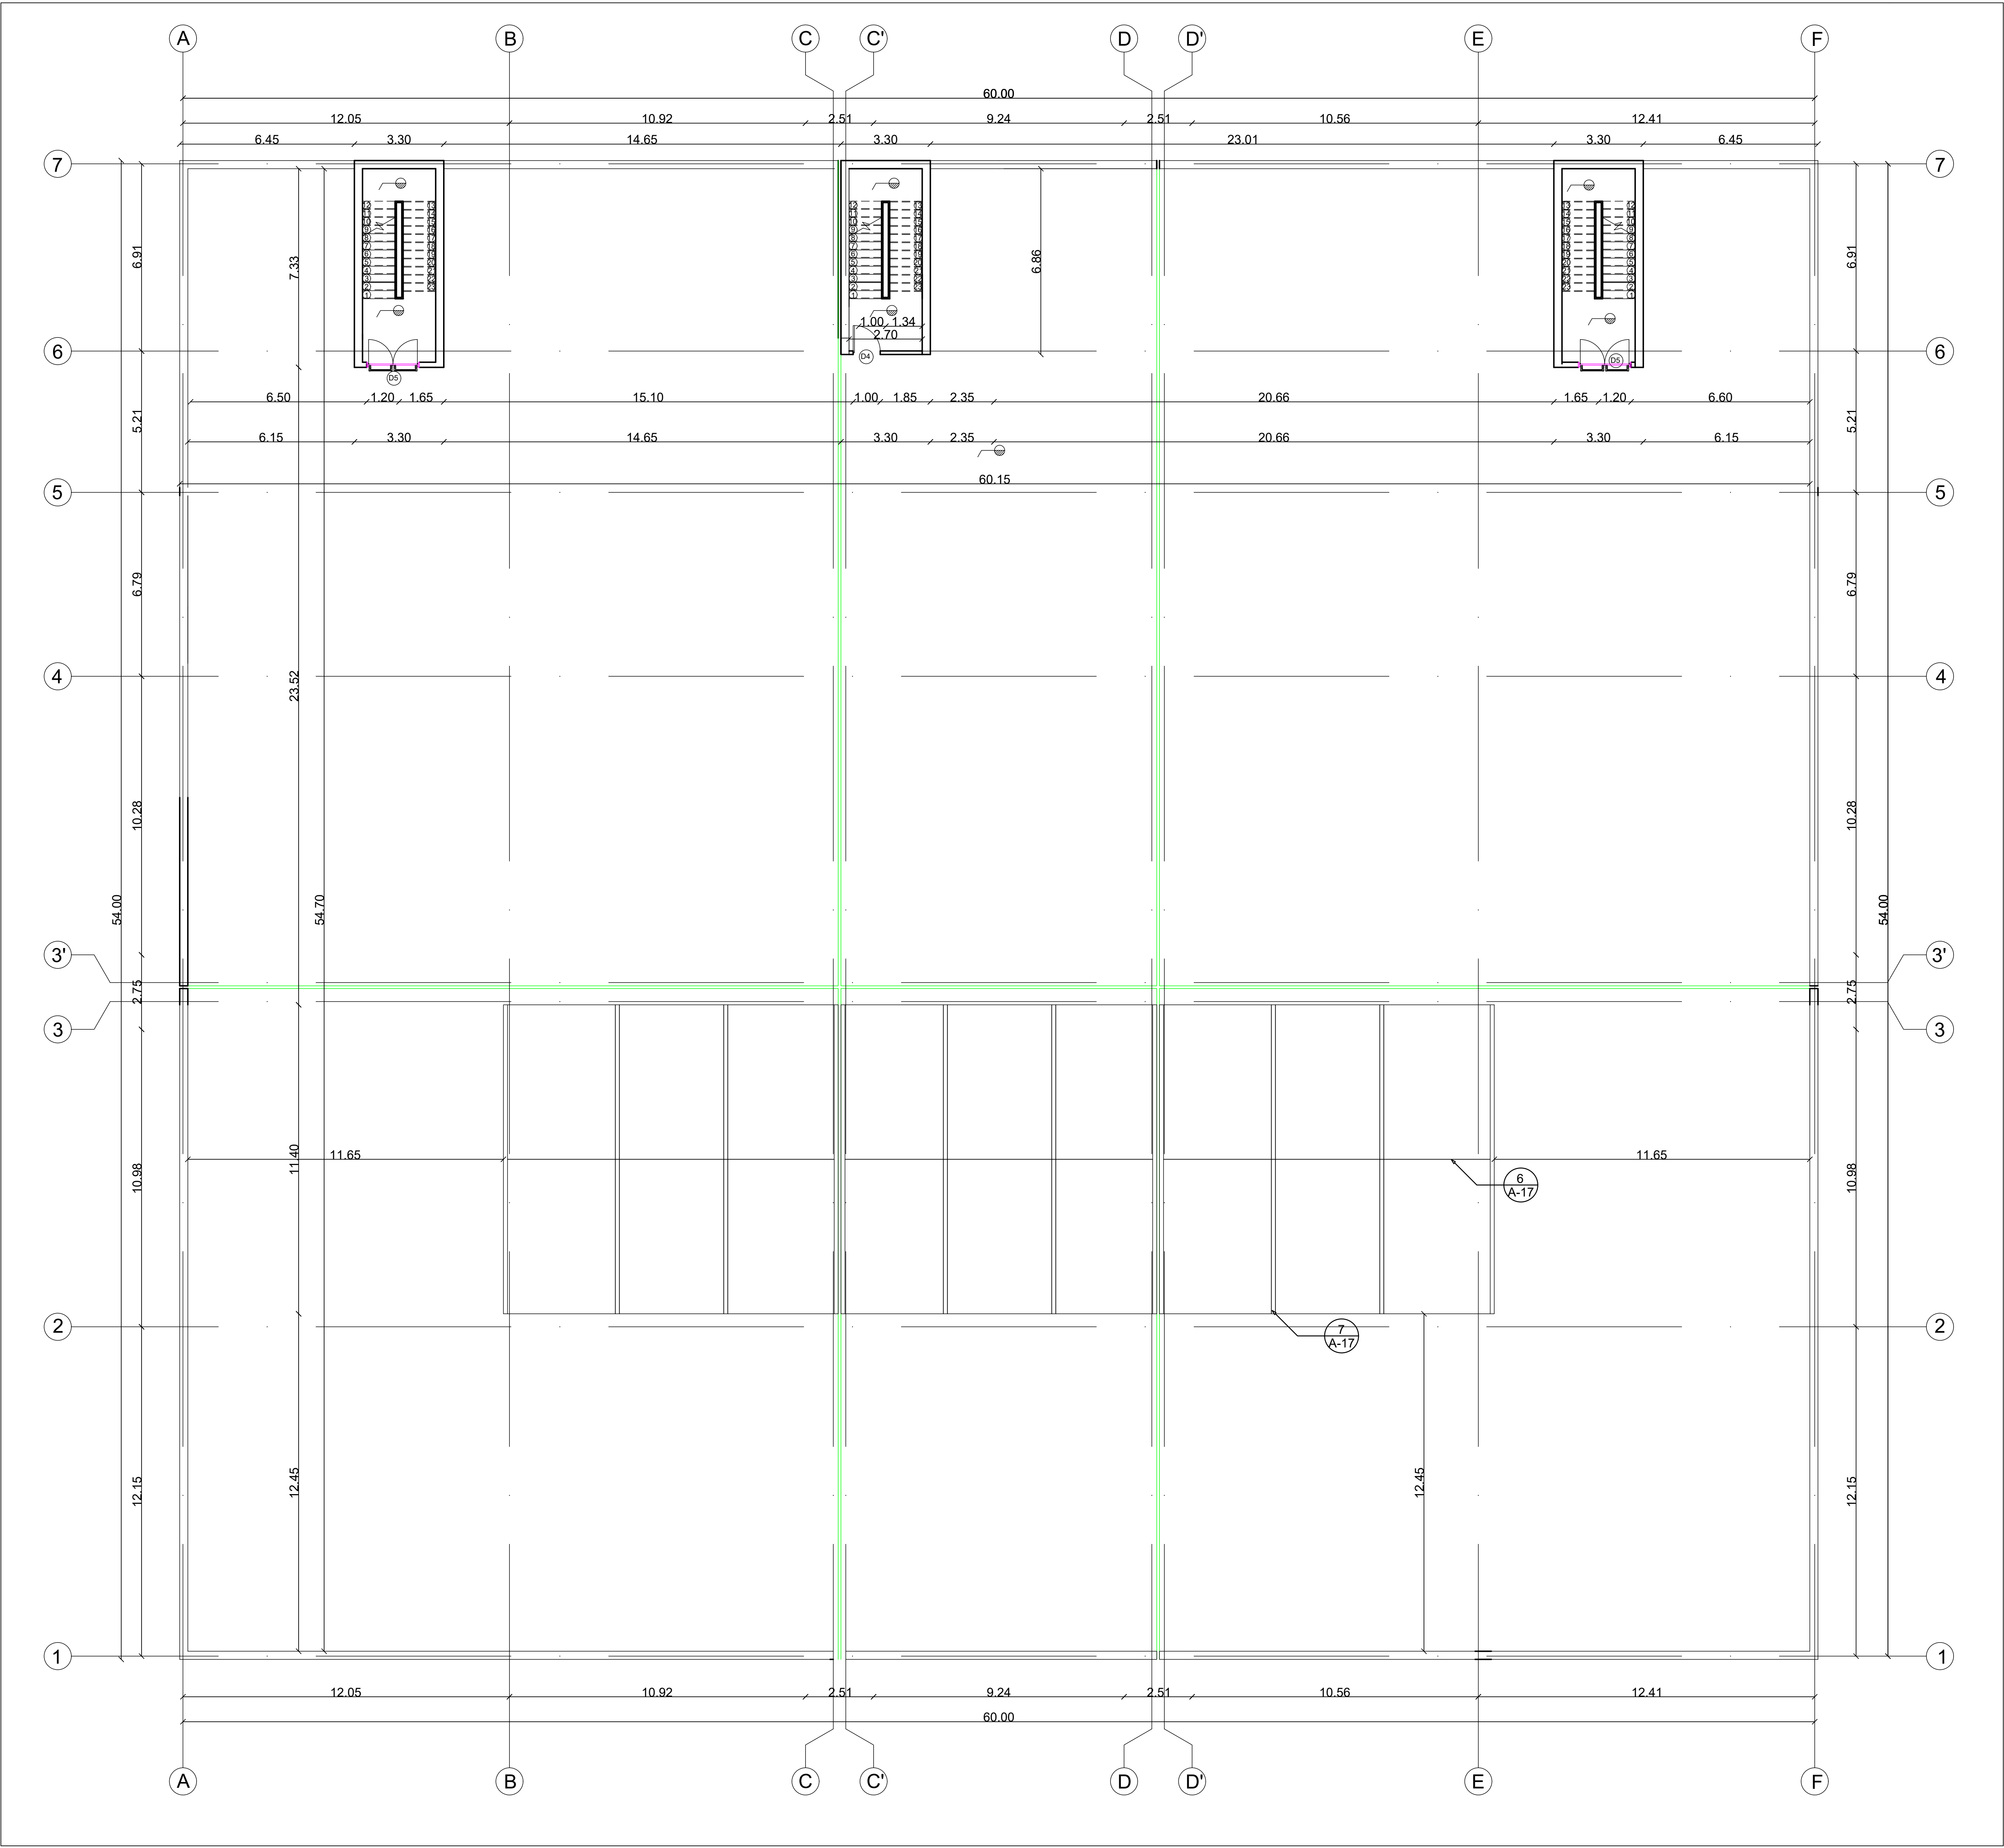

Window types		
name	width	Material
W1	0.5 M	Aluminum frame ,Hooper
W2	1.0 M	Aluminum frame ,sliding
W3	2.0 M	Aluminum frame ,sliding
W4	0.5 M	Aluminum frame ,Awning

Door types		
name	width	Material
D1	2.00 M	Glass Hinged door,2leaf
D2	2.00 M	Glass acoustic door,2leaf
D3	2.00 M	Glass Sliding door,2leaf
D4	1.00 M	Wooden hinged door,1leaf
D5	2.00 M	Panic bar Aluminum Sliding door,2leaf

Finishing materials		
Type	No.	Description
Ceiling	1	Plaster Gypsum
	2	False ceiling tiles
	3	Paint
Walls	1	Fiberglass board 25mm,(1")thick
	2	Ceramic tiles 60x60x0.8cm
	3	Paint
	4	Wood panels,tounge and grove decking
Skirting	1	wooden skirting
	2	Ceramic tiles 60x60x0.8cm
	3	Marble skirting
Flooring	1	Paint
	2	Carpet
	3	Ceramic tiles 60x60x0.8cm
	4	Vinyl tiles



OCTOBER UNIVERSITY
FOR MODERN SCIENCES & ARTS
Architectural Engineering Department
Fall 2022

Faculty Info

Instructors:
Dr. Tarek Galal

Assistant:
Eng.

Assignment No. :

Roof floor plan Scale 1:100


Date: / / 2023

Week Number:

Student Name: Abdullah refat

ID: 195267

A-07

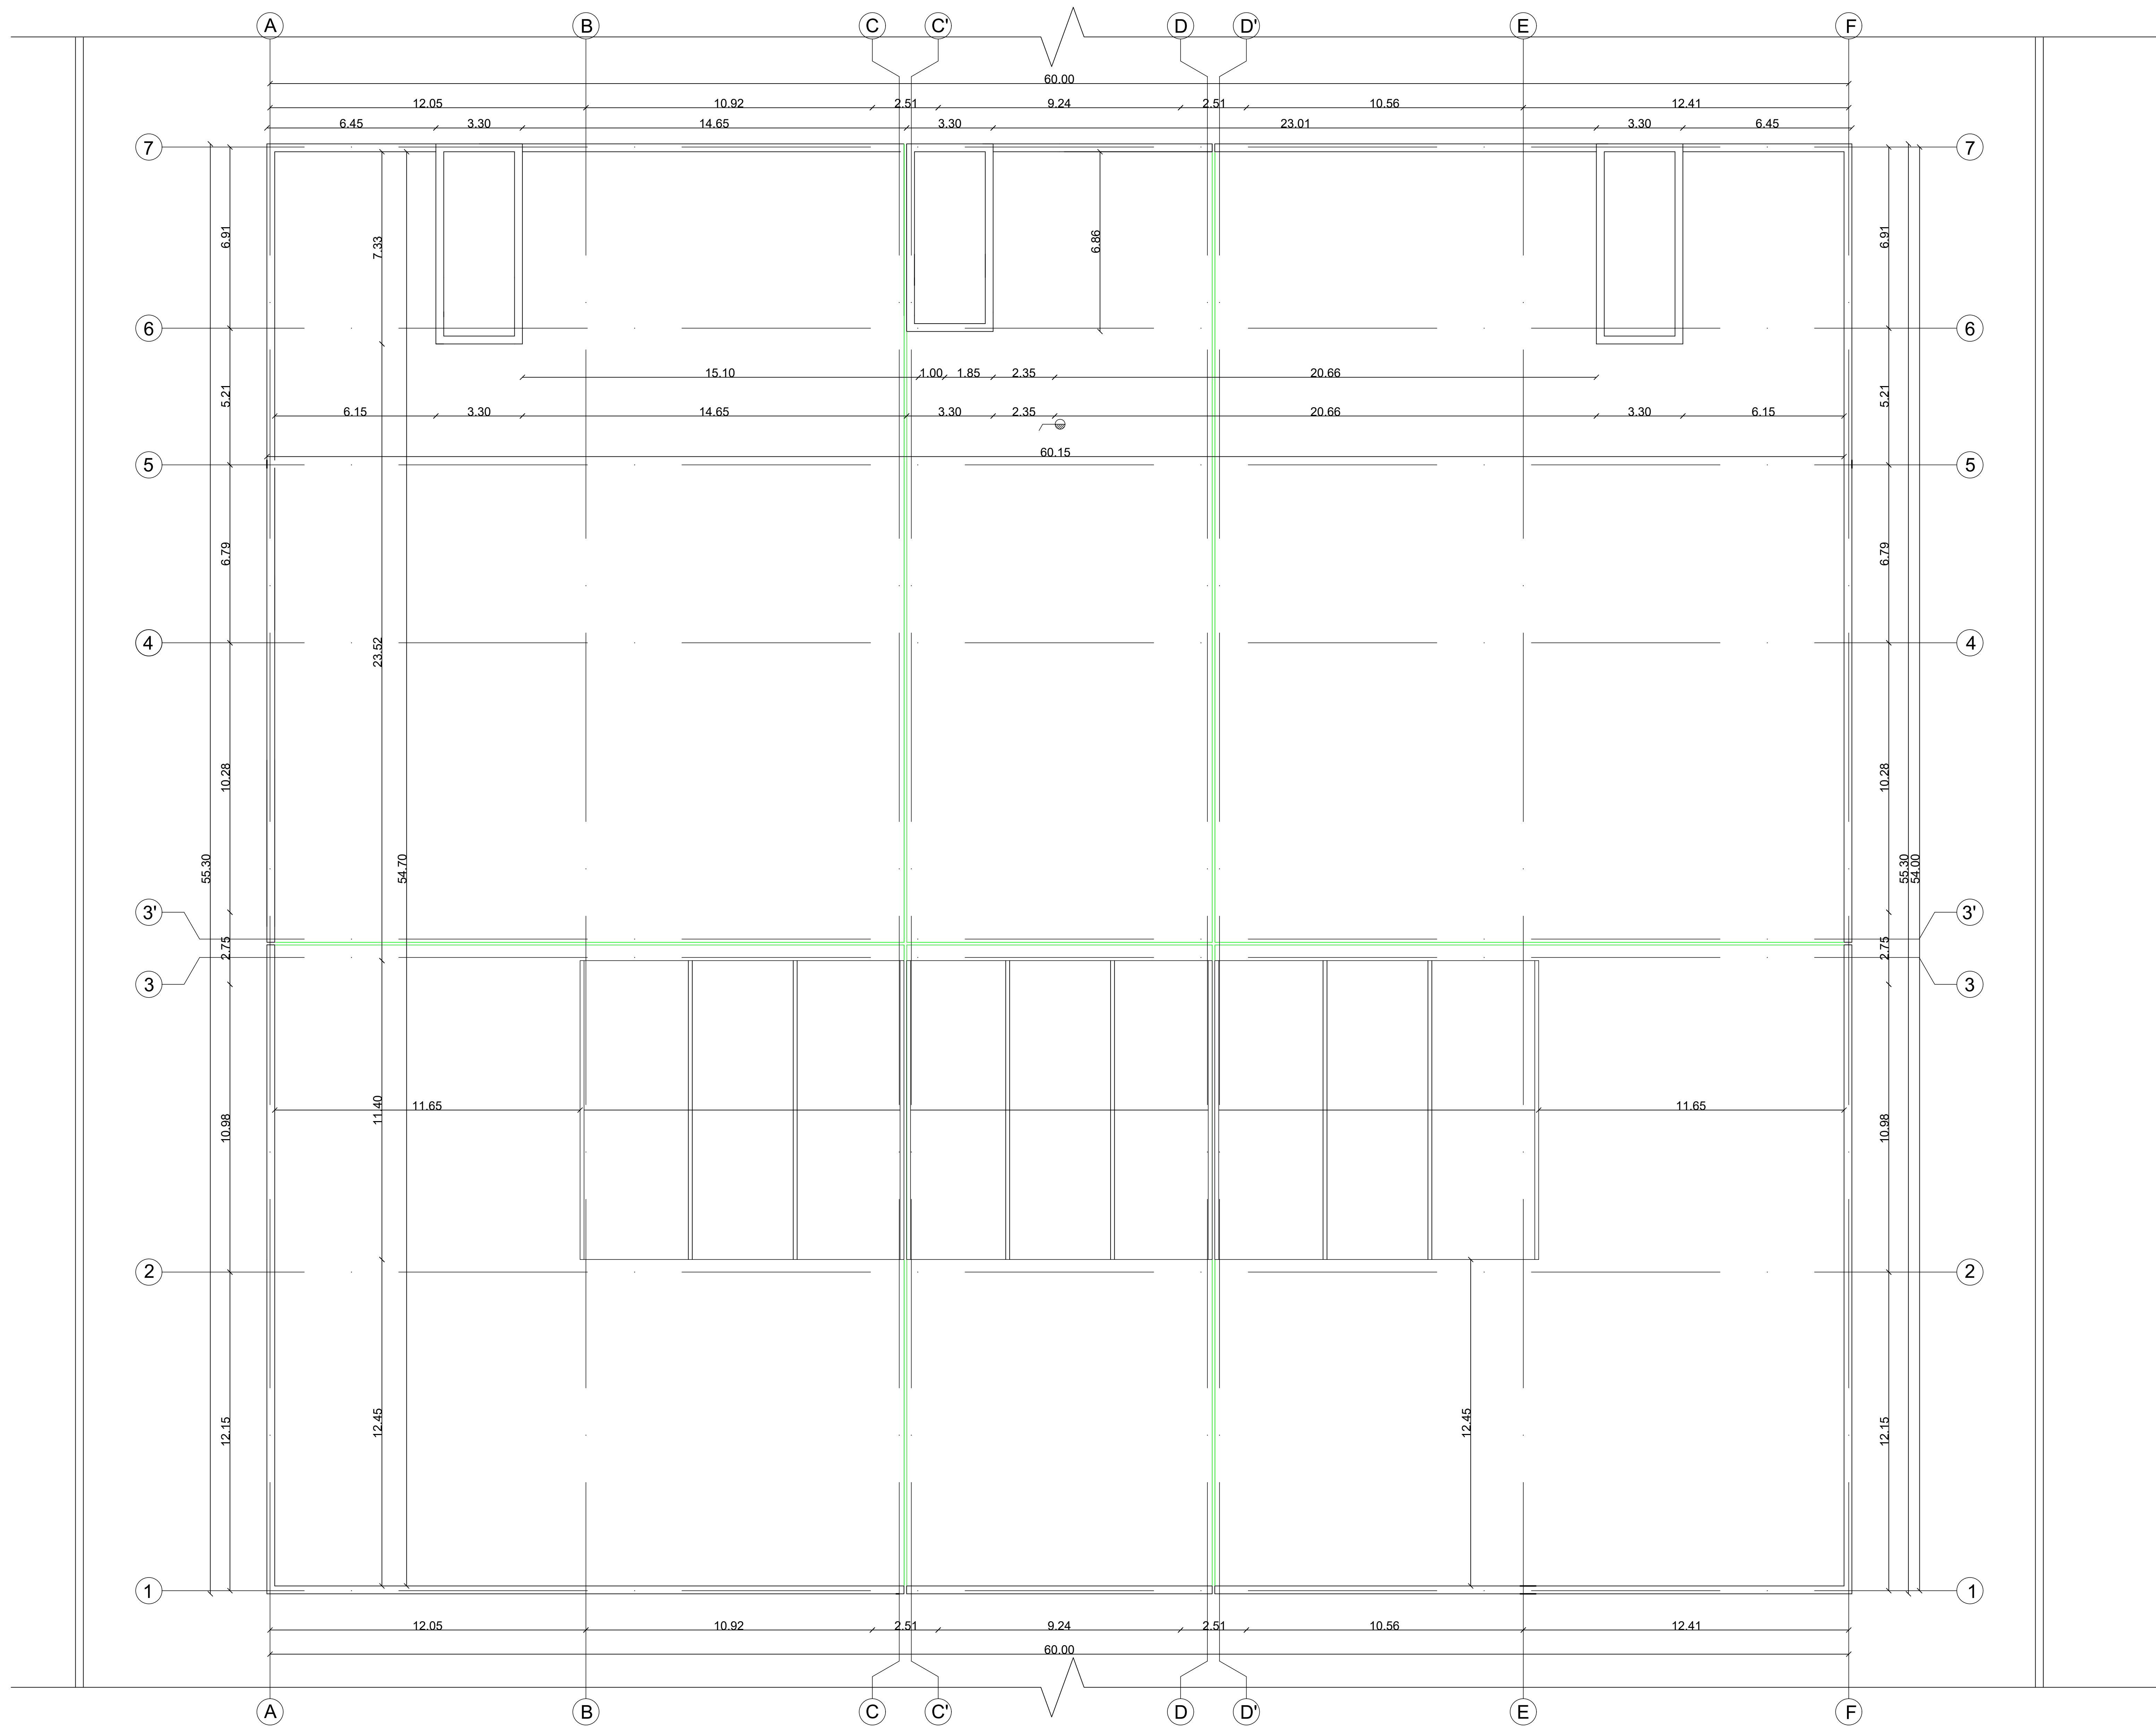

OCTOBER UNIVERSITY
FOR MODERN SCIENCES & ARTS
Architectural Engineering Department
Fall 2022

Faculty Info

Instructors:
Dr. Tarek Galal

Assistant:
Eng.

Assignment No. :

Site plan Scale
1:100

Date: / / 2023

Week Number:

Student Name: Abdullah refat

ID: 195267

A-08