



Instructors:
Dr. Tarek Gala

Assistant:
Eng.

Assignment No. :

West elevation
Scale 1:100


Date: / / 2023

Week Number:

Student Name: Abdullah refat

ID: 195267



A-10

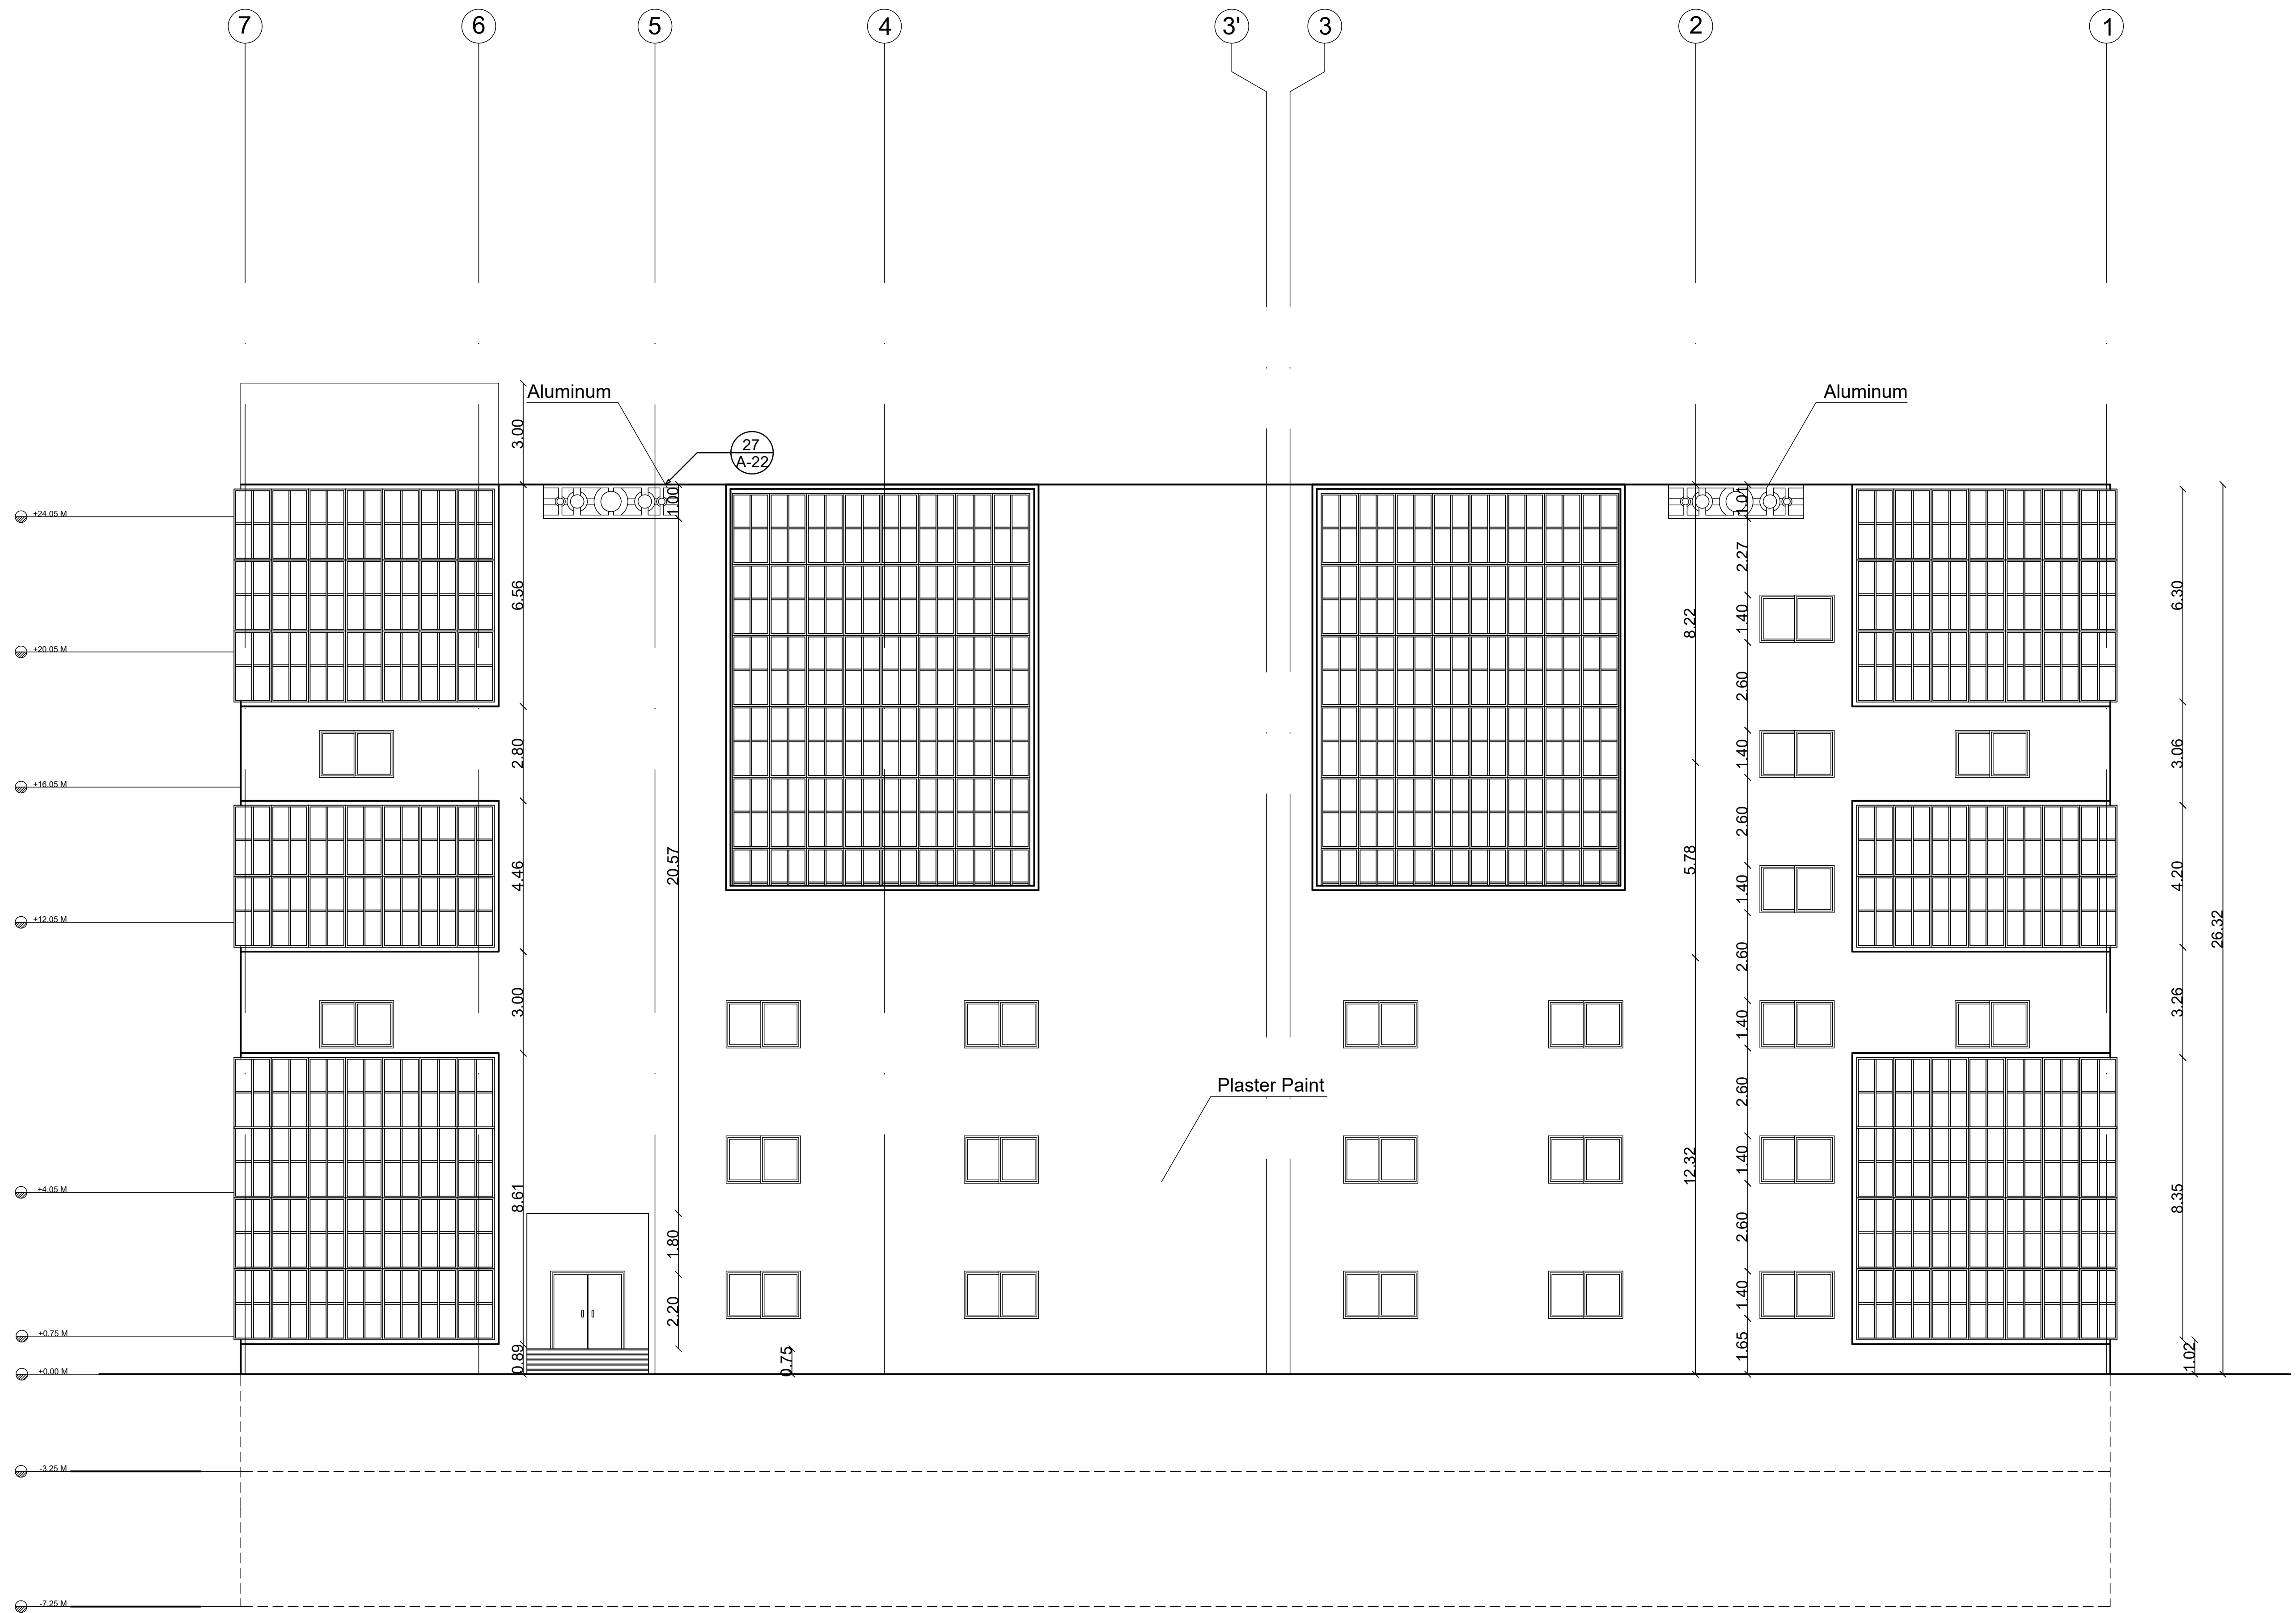

Window types		
name	width	Material
W1	0.5 M	Aluminum frame ,Hooper
W2	1.0 M	Aluminum frame ,sliding
W3	2.0 M	Aluminum frame ,sliding
W4	0.5 M	Aluminum frame ,Awning

Door types		
name	width	Material
D1	1.00 M	Wooden acoustic door,1leaf
D2	0.80 M	Wooden acoustic door,1leaf
D3	0.80 M	Wooden acoustic door,1leaf
D4	2.00 M	Aluminum Sliding door,2leaf

Finishing materials			
Type	No.	Description	
Ceiling	1	Plaster Gypsum	
	2	False ceiling tiles	
	3	Paint	
Walls	1	Fiberglass board .25mm,(1")thick	
	2	Ceramic tiles 60x60x0.8cm	
	3	Paint	
	4	Wood panels,tounge and grove decking	
Skirting	1	wooden skirting	
	2	Ceramic tiles 60x60x0.8cm	
	3	Marble skirting	
Flooring	1	Paint	
	2	Carpet	
	3	Ceramic tiles 60x60x0.8cm	
	4	Vinyl tiles	

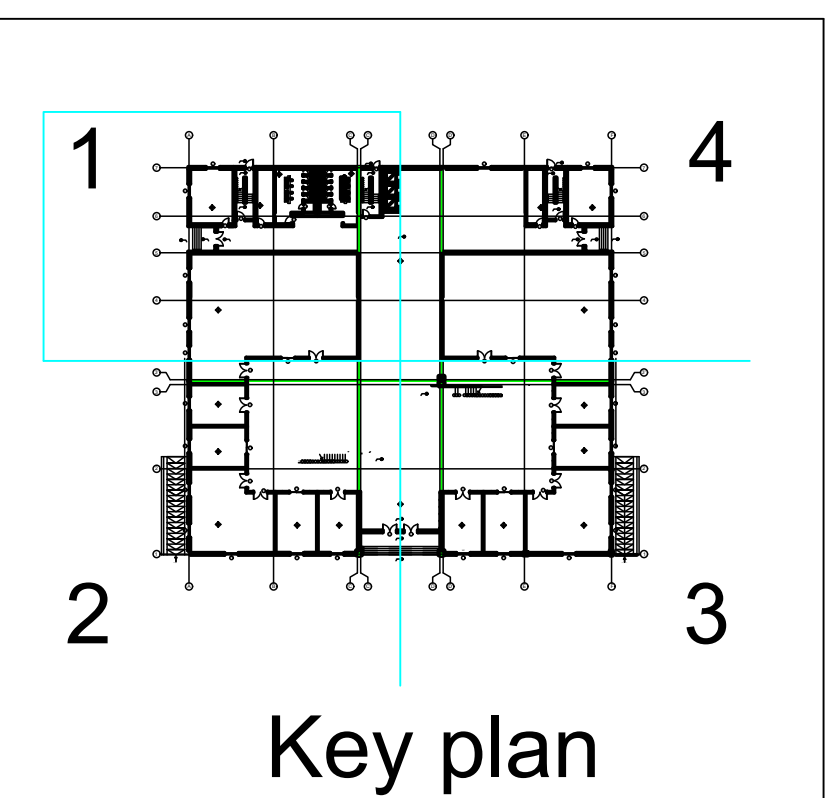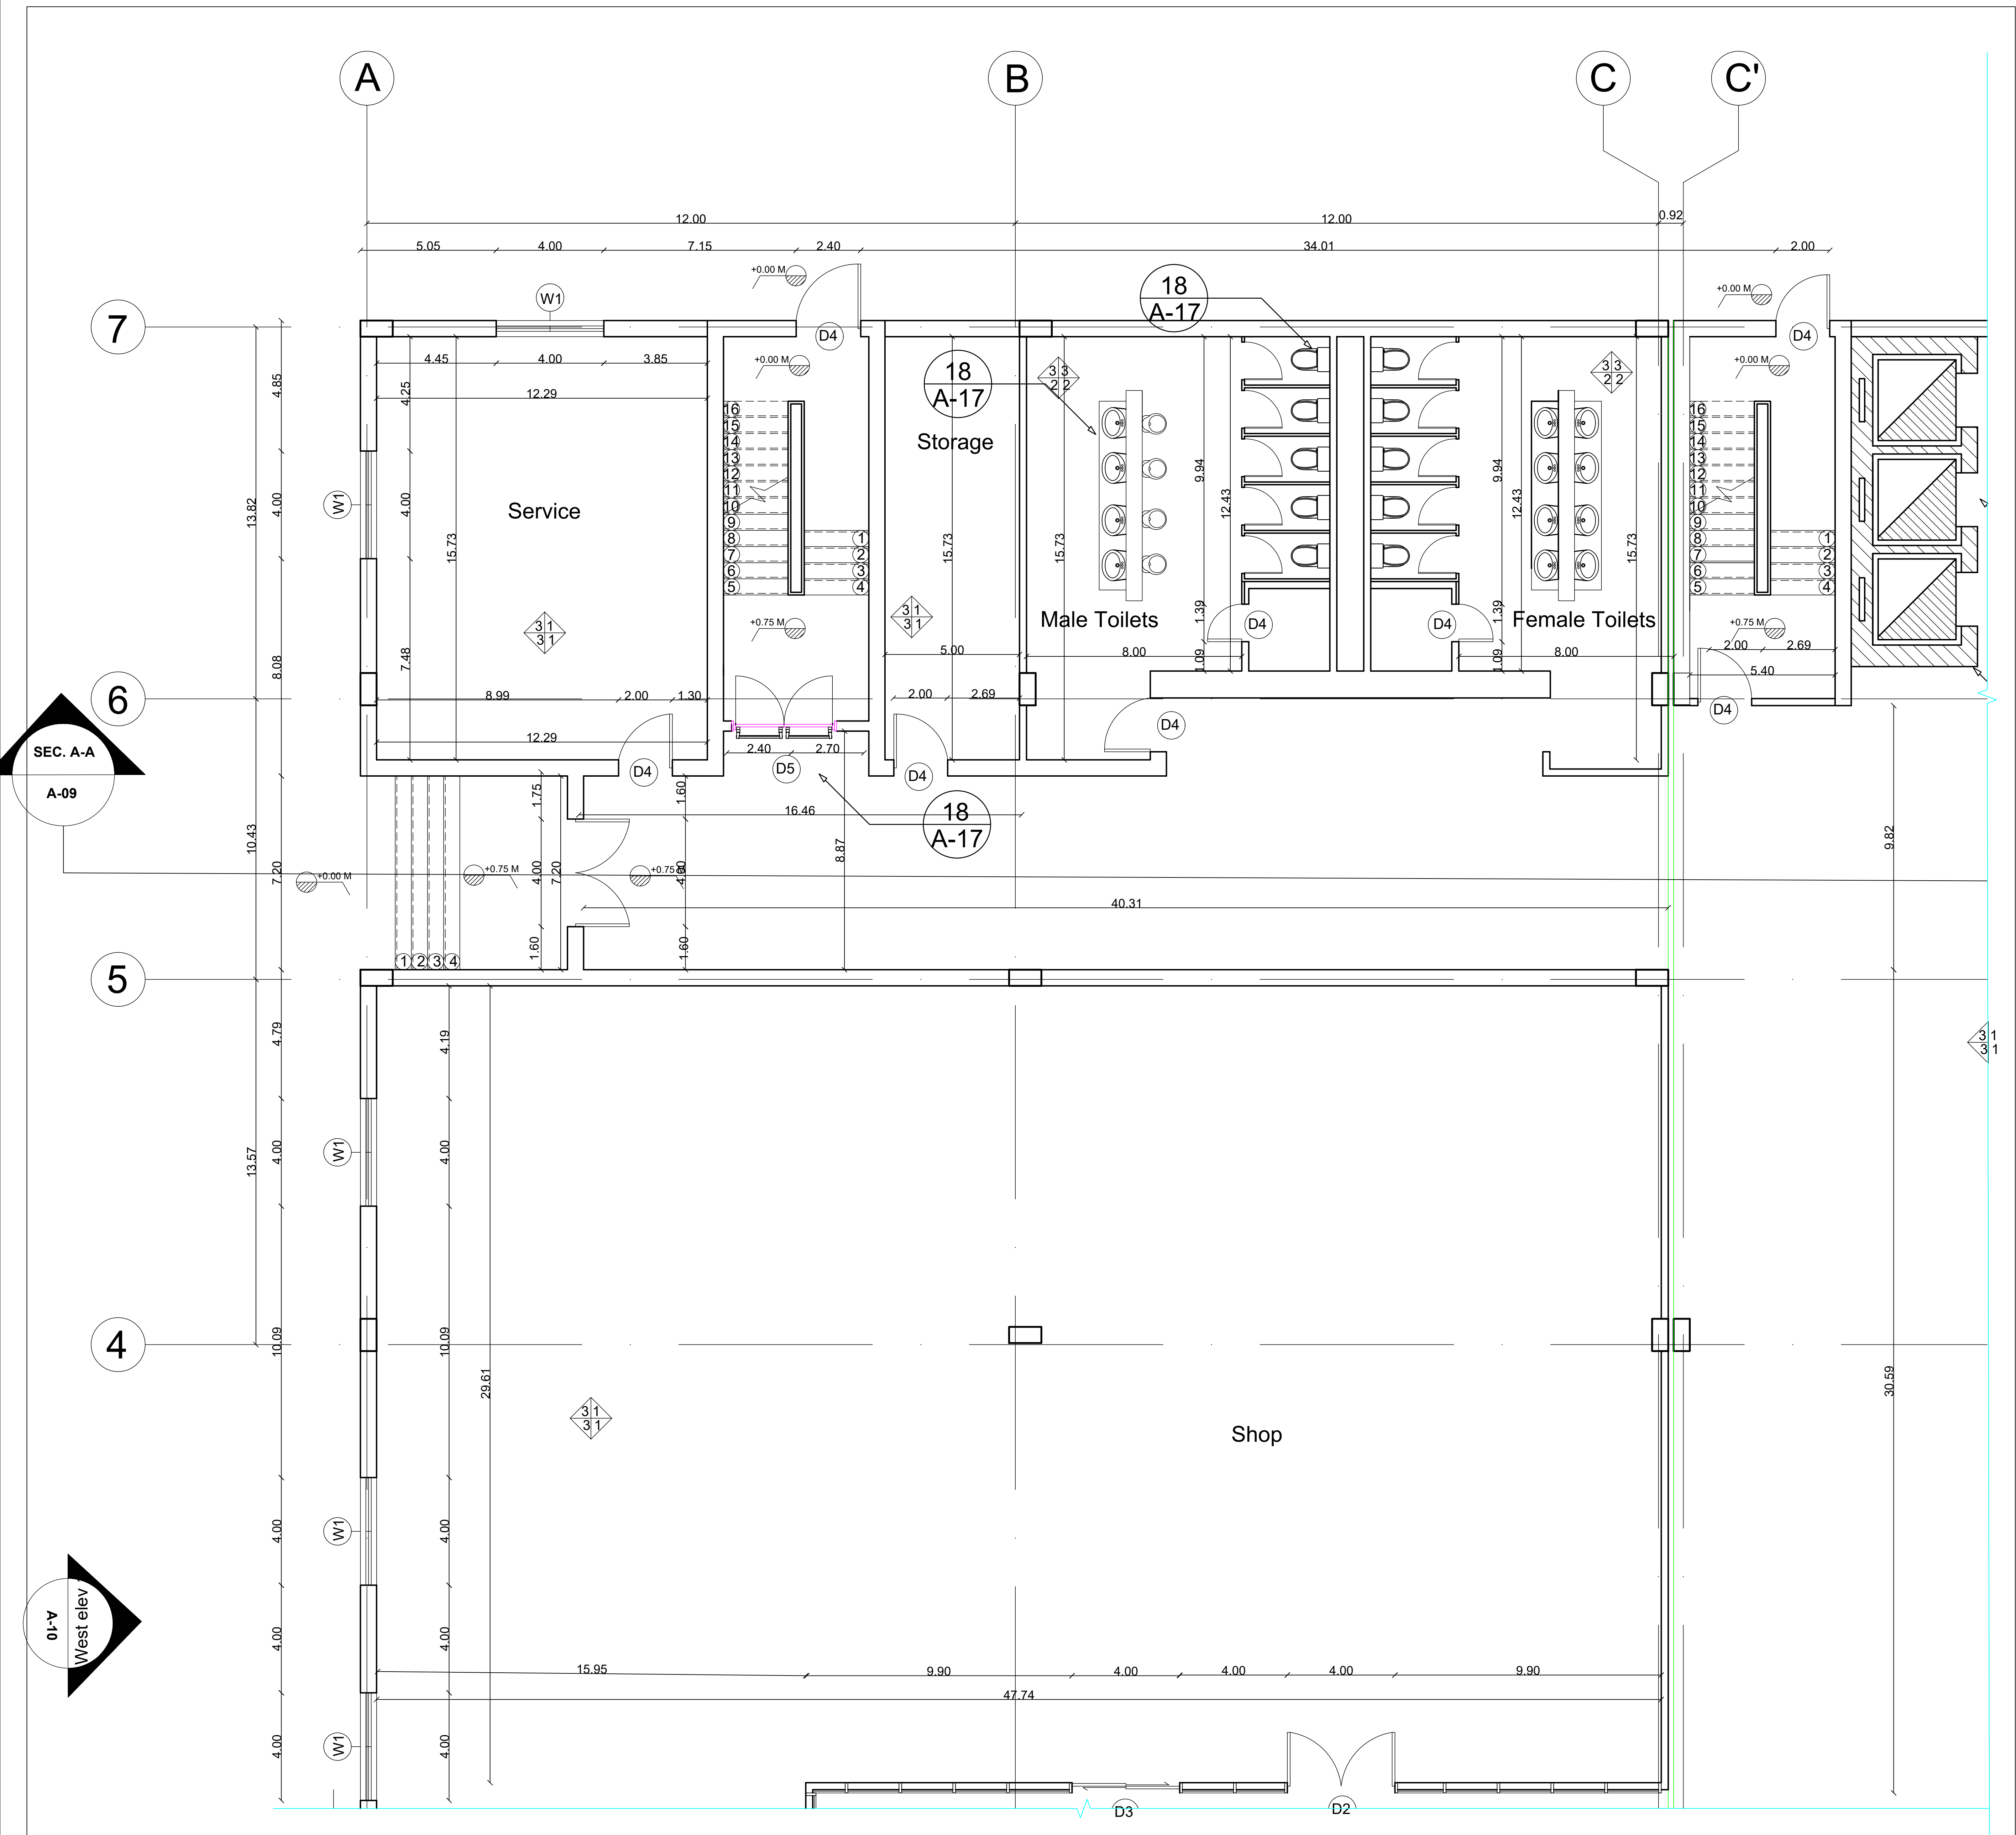

Key plan



OCTOBER UNIVERSITY
FOR MODERN SCIENCES & ARTS
Architectural Engineering Department
Fall 2022

Faculty Info

Instructors:
Dr. Tarek Galal

Assistant:
Eng.

Assignment No. :

Ground floor plan Scale 1:50, 1st quarter

Date: / / 2023

Week Number:

Student Name: Abdullah refat



ID: 195267

Window types		
name	width	Material
W1	0.5 M	Aluminum frame ,Hooper
W2	1.0 M	Aluminum frame ,sliding
W3	2.0 M	Aluminum frame ,sliding
W4	0.5 M	Aluminum frame ,Awning

Door types		
name	width	Material
D1	1.00 M	Wooden acoustic door,1leaf
D2	0.80 M	Wooden acoustic door,1leaf
D3	0.80 M	Wooden acoustic door,1leaf
D4	2.00 M	Aluminum Sliding door,2leaf

Finishing materials		
Type	No.	Description
Ceiling	1	Plaster Gypsum
	2	False ceiling tiles
	3	Paint
Walls	1	Fiberglass board 25mm,(1")thick
	2	Ceramic tiles 60x60x0.8cm
	3	Paint
Skirting	1	wooden skirting
	2	Ceramic tiles 60x60x0.8cm
	3	Marble skirting
Flooring	1	Paint
	2	Carpet
	3	Ceramic tiles 60x60x0.8cm
	4	Vinyl tiles

A-11

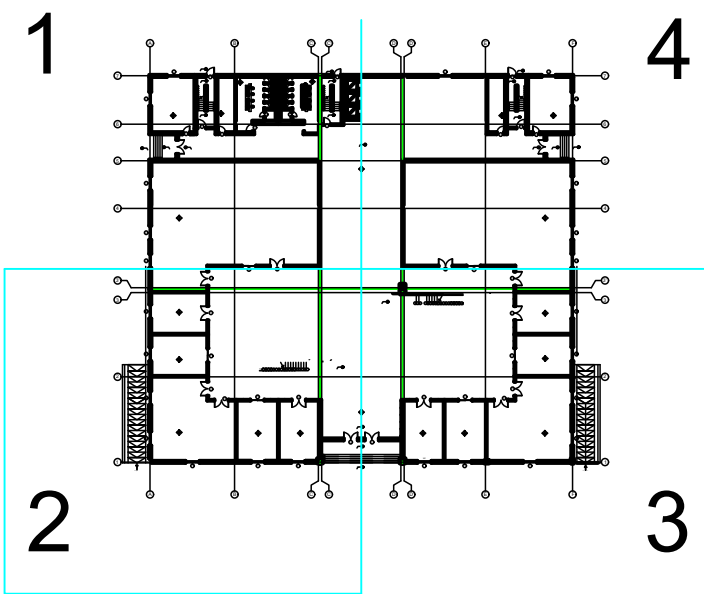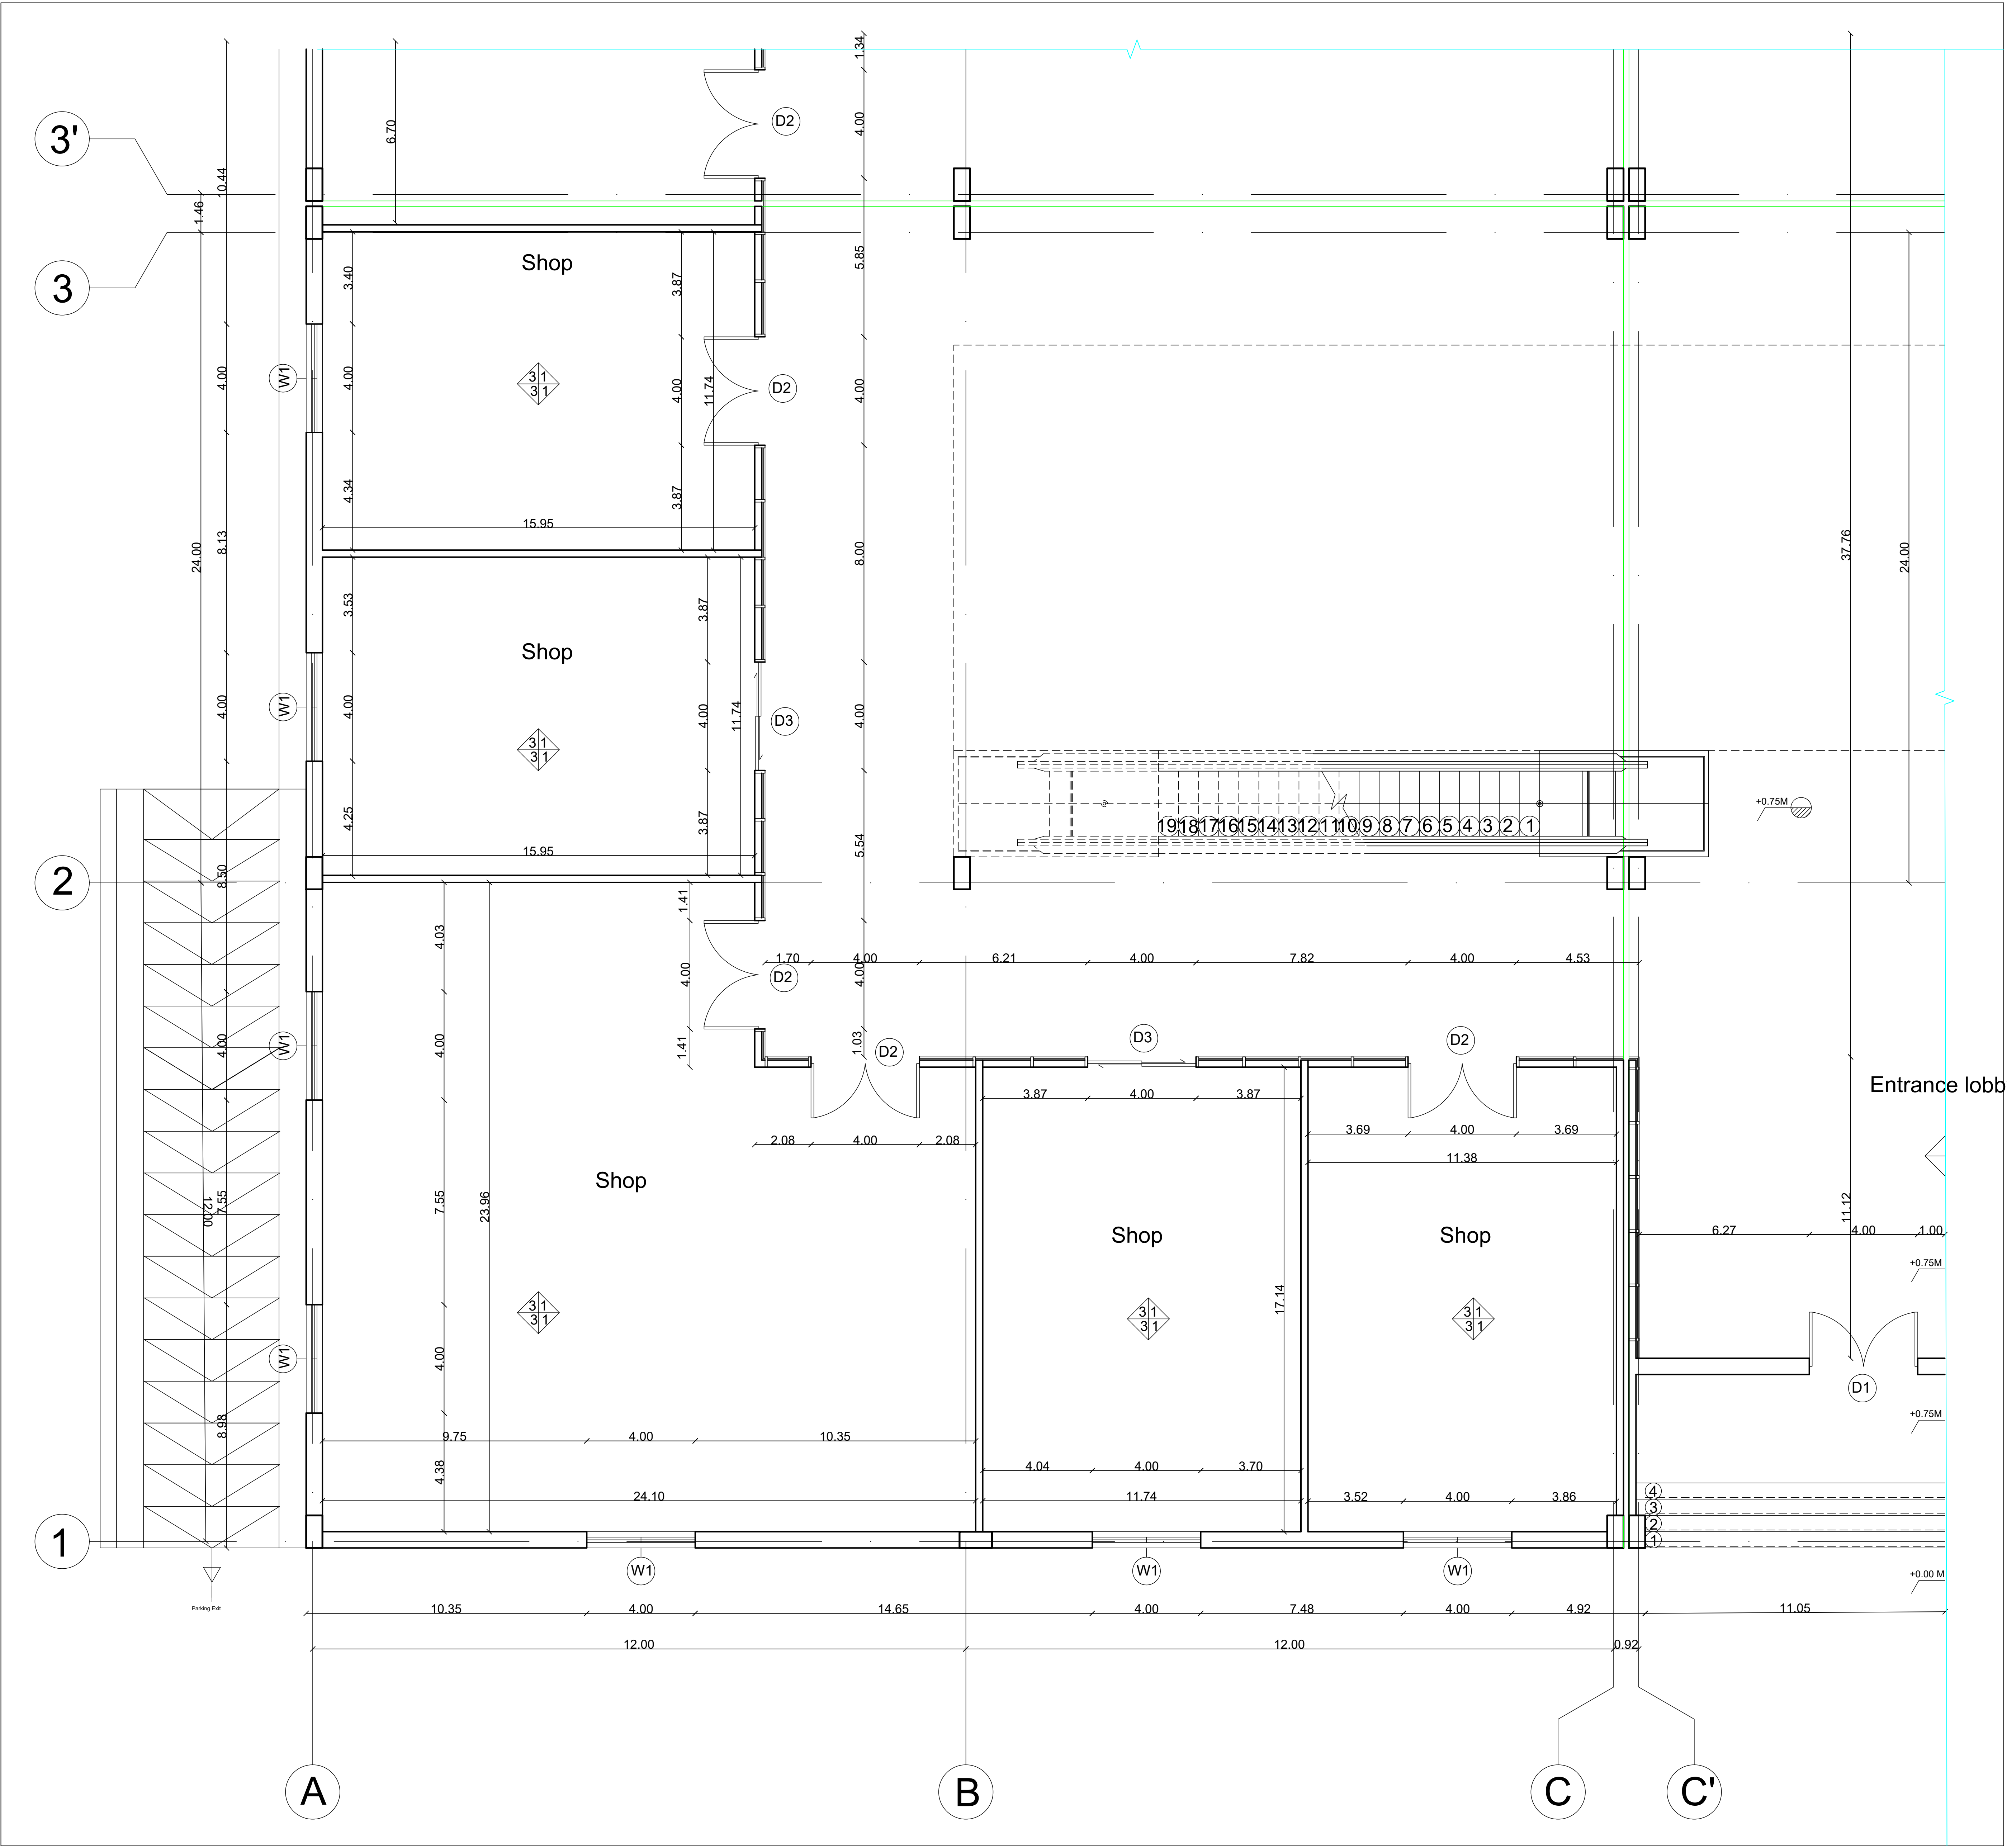

Key plan



OCTOBER UNIVERSITY
FOR MODERN SCIENCES & ARTS
Architectural Engineering Department
Fall 2022

Faculty Info

Instructors:
Dr. Tarek Galal

Assistant:
Eng.

Assignment No. :

Ground floor plan
Scale 1:50, 2nd
quarter

Date: / / 2023

Week Number:


Student Name: Abdullah refat

ID: 195267

Window types		
name	width	Material
W1	0.5 M	Aluminum frame ,Hooper
W2	1.0 M	Aluminum frame ,sliding
W3	2.0 M	Aluminum frame ,sliding
W4	0.5 M	Aluminum frame ,Awning

Door types		
name	width	Material
D1	1.00 M	Wooden acoustic door,1leaf
D2	0.80 M	Wooden acoustic door,1leaf
D3	0.80 M	Wooden acoustic door,1leaf
D4	2.00 M	Aluminum Sliding door,2leaf

Finishing materials		
Type	No.	Description
Ceiling	1	Plaster Gypsum
	2	False ceiling tiles
	3	Paint
Walls	1	Fiberglass board 25mm,(1")thick
	2	Ceramic tiles 60x60x0.8cm
	3	Paint
	4	Wood panels,tounge and grove decking
Skirting	1	wooden skirting
	2	Ceramic tiles 60x60x0.8cm
	3	Marble skirting
Flooring	1	Paint
	2	Carpet
	3	Ceramic tiles 60x60x0.8cm
	4	Vinyl tiles

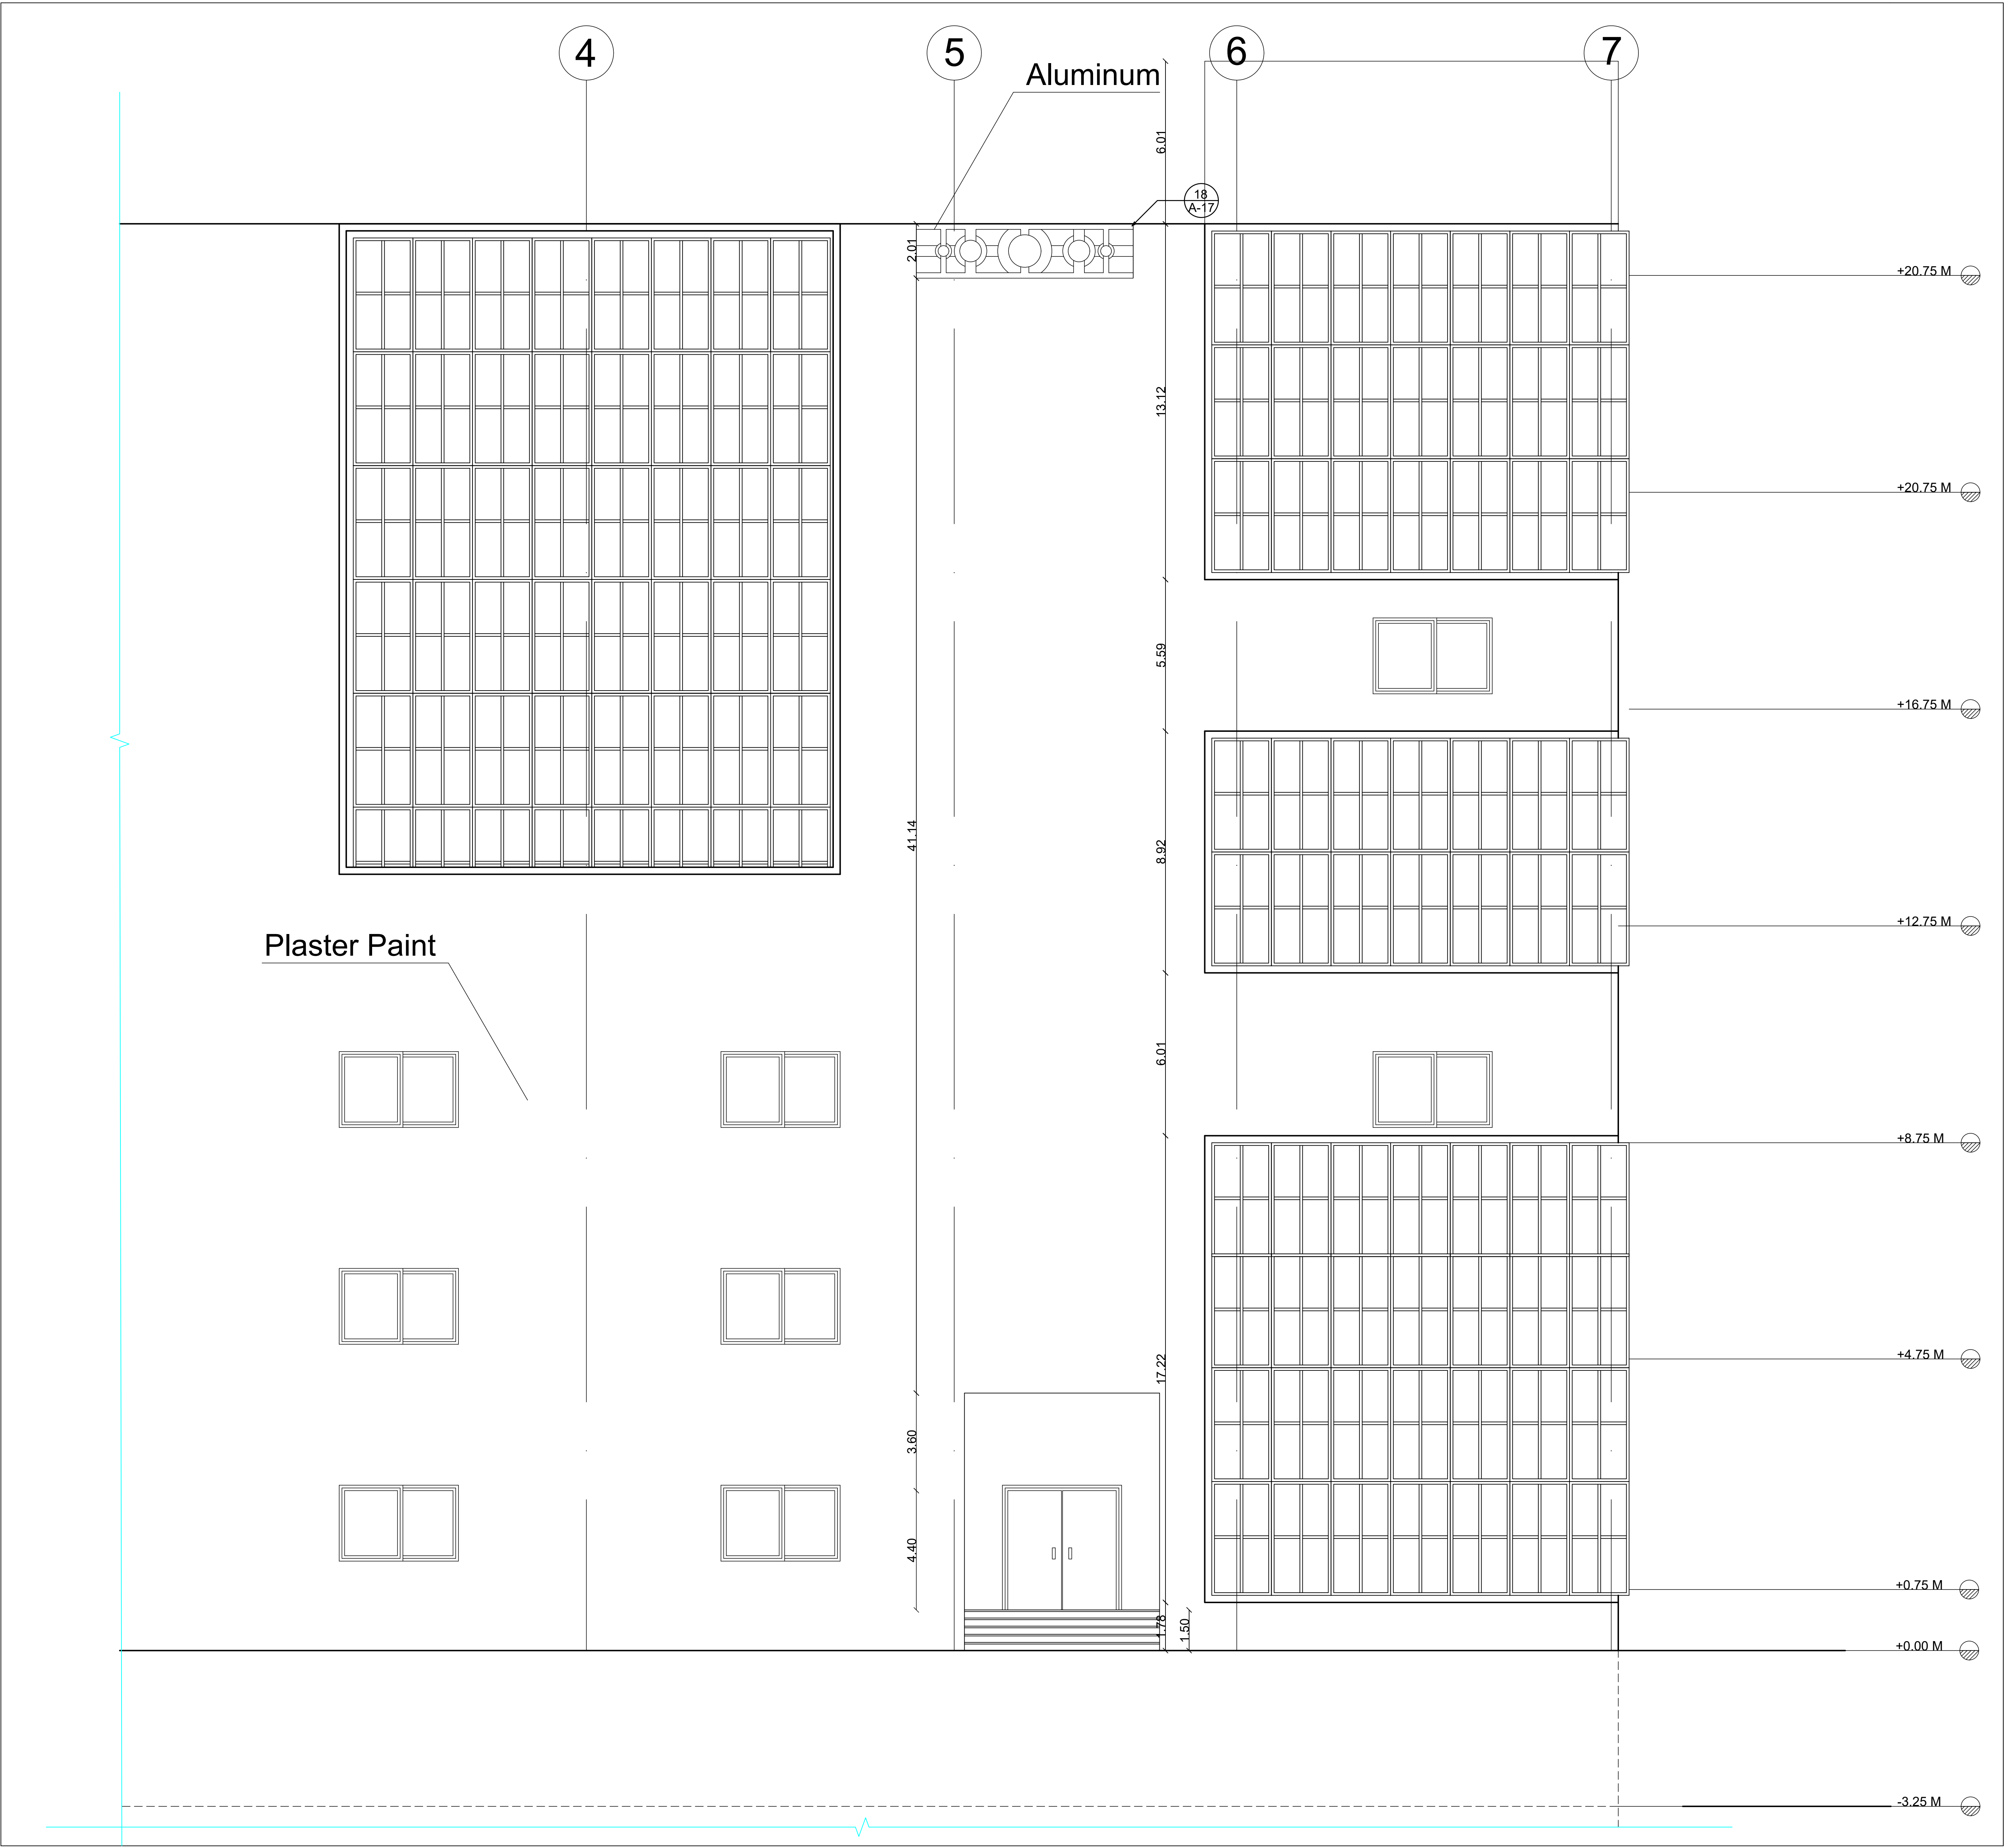

OCTOBER UNIVERSITY
FOR MODERN SCIENCES & ARTS
Architectural Engineering Department
Fall 2022

Faculty Info

Instructors:
Dr. Tarek Galal

Assistant:
Eng.

Assignment No. :

East elevation Scale 1:50

Date: / / 2023

Week Number:

Student Name: Abdullah refat


ID: 195267

Window types		
name	width	Material
W1	0.5 M	Aluminum frame ,Hooper
W2	1.0 M	Aluminum frame ,sliding
W3	2.0 M	Aluminum frame ,sliding
W4	0.5 M	Aluminum frame ,Awning

Door types		
name	width	Material
D1	1.00 M	Wooden acoustic door,1leaf
D2	0.80 M	Wooden acoustic door,1leaf
D3	0.80 M	Wooden acoustic door,1leaf
D4	2.00 M	Aluminum Sliding door,2leaf

Finishing materials		
Type	No.	Description
Ceiling	1	Plaster Gypsum
	2	False ceiling tiles
	3	Paint
Walls	1	Fiberglass board 25mm,(1")thick
	2	Ceramic tiles 60x60x0.8cm
	3	Paint
	4	Wood panels,tounge and grove decking
Skirting	1	wooden skirting
	2	Ceramic tiles 60x60x0.8cm
	3	Marble skirting
Flooring	1	Paint
	2	Carpet
	3	Ceramic tiles 60x60x0.8cm
	4	Vinyl tiles

A-13

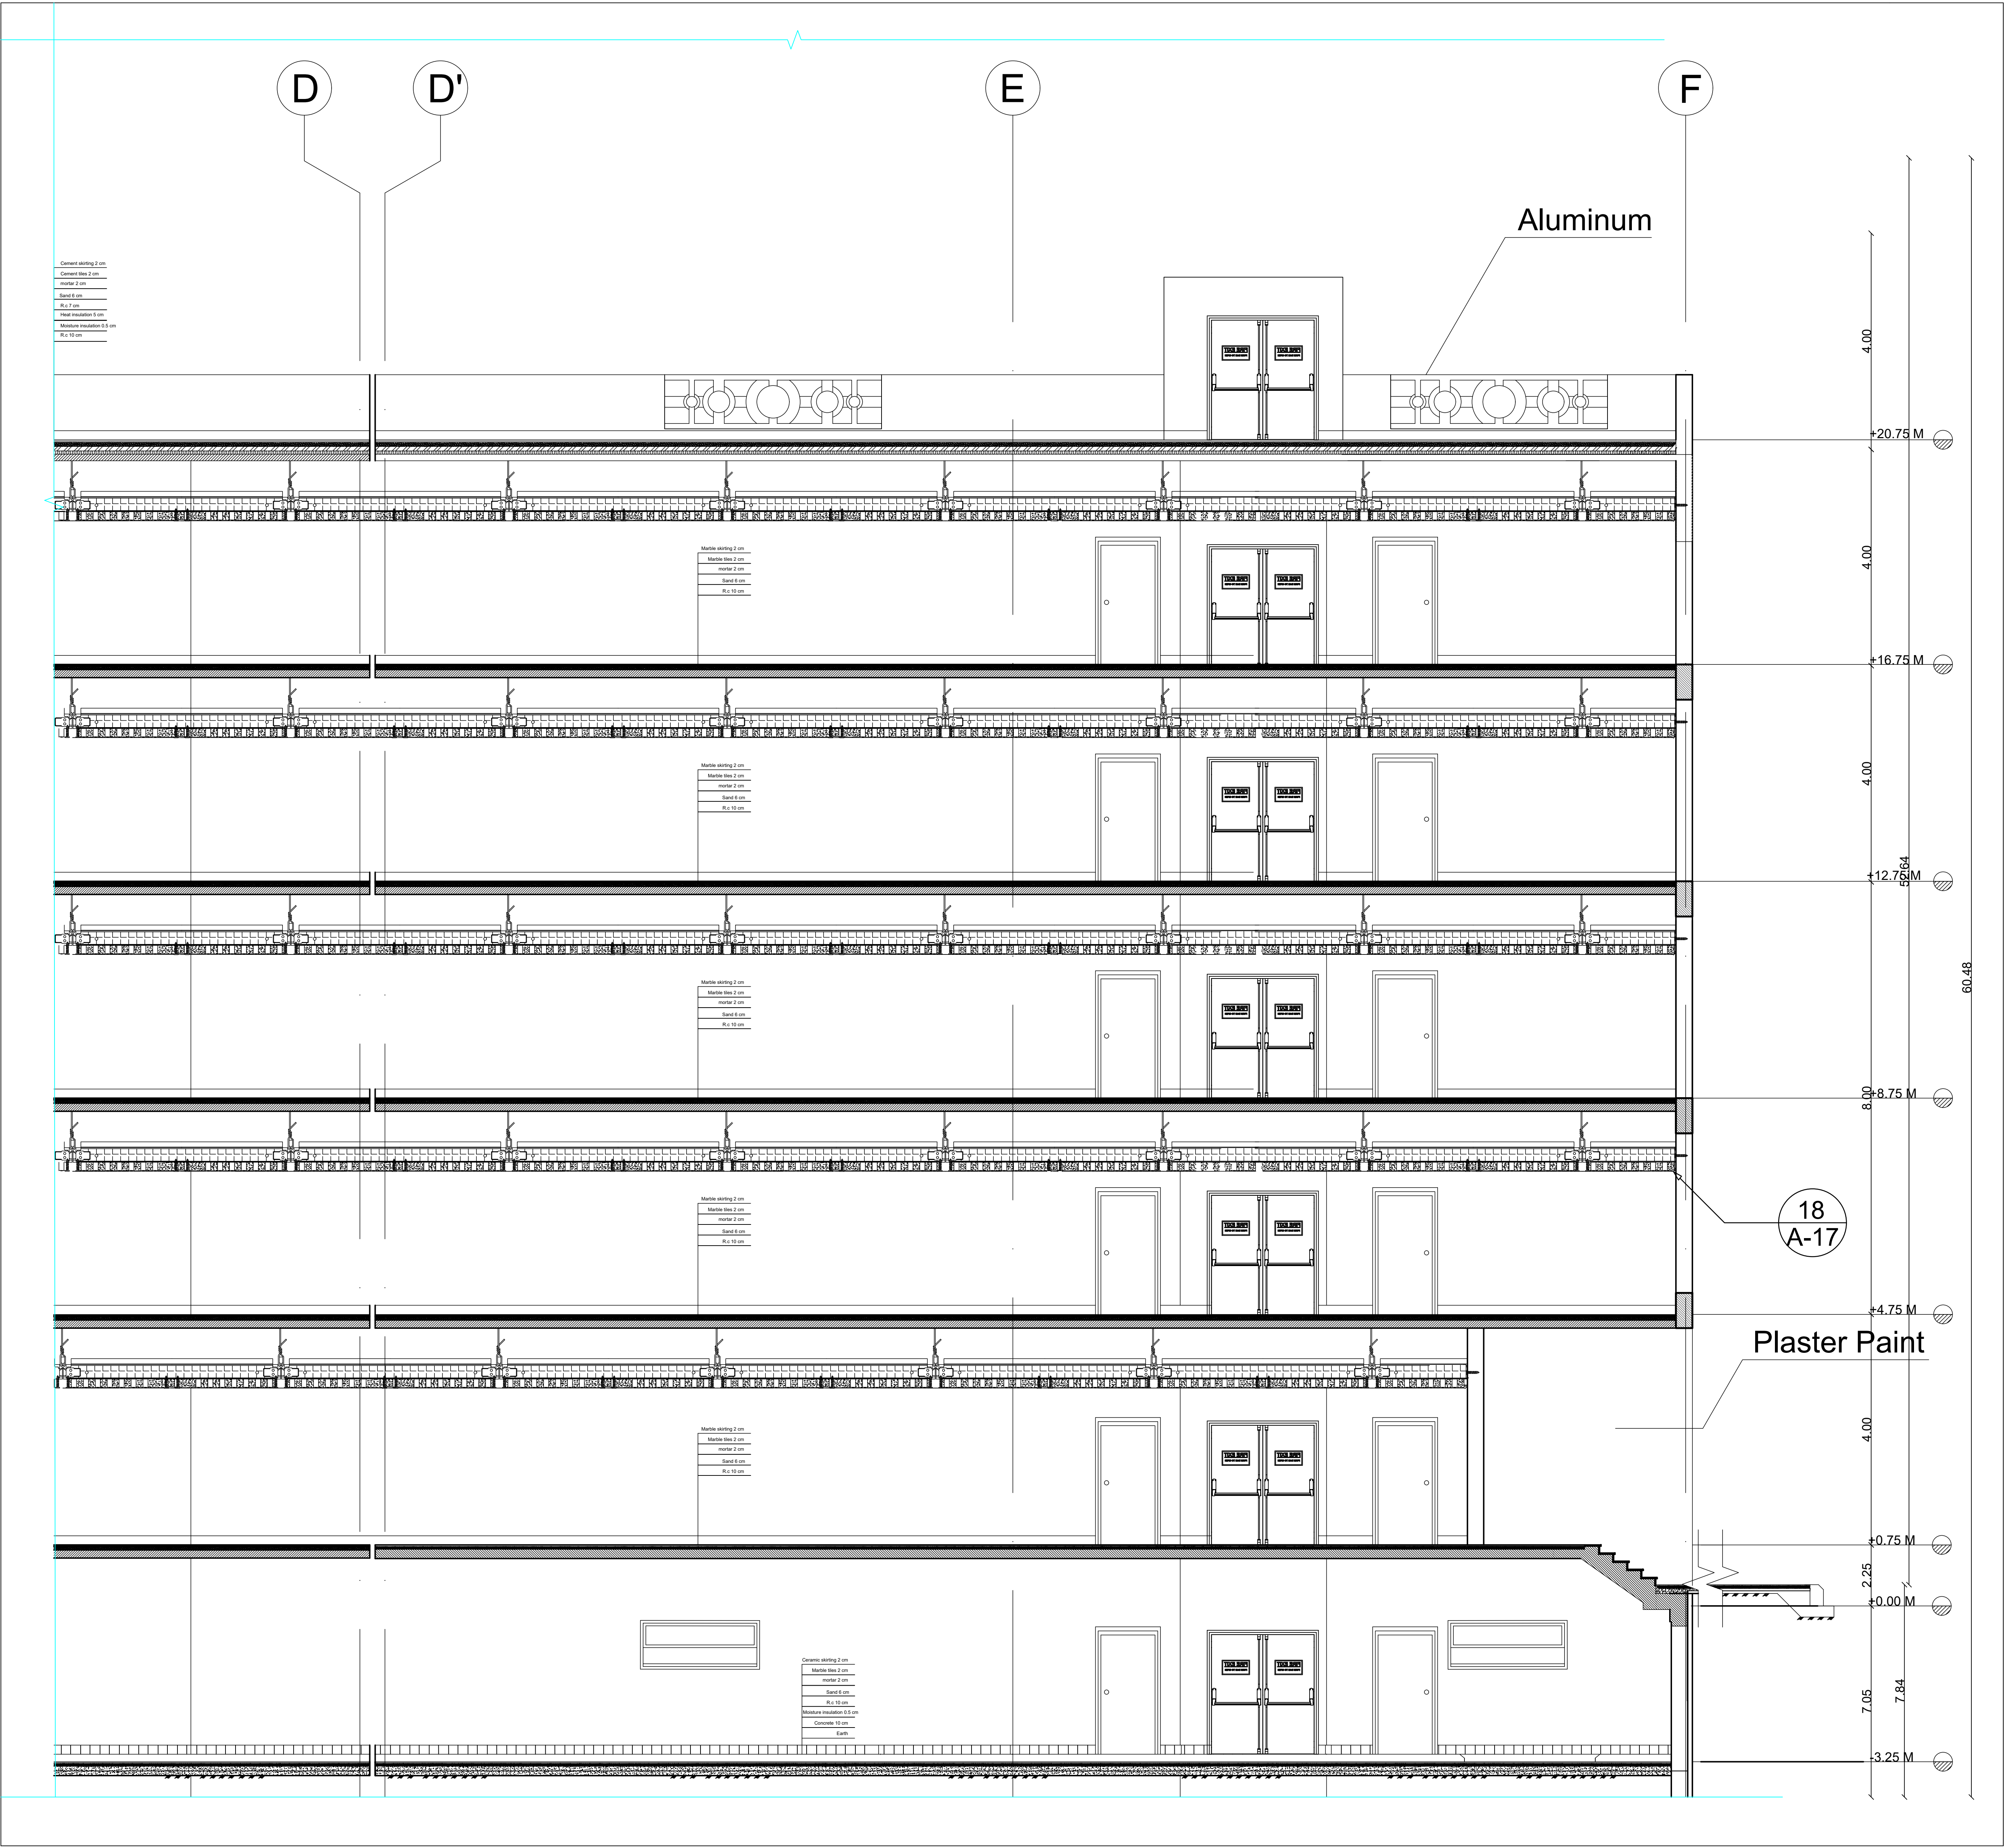

OCTOBER UNIVERSITY
FOR MODERN SCIENCES & ARTS
Architectural Engineering Department
Fall 2022

Faculty Info

Instructors:
Dr. Tarek Galal

Assistant:
Eng.

Assignment No. :

Cross section A-A Scale 1:50

Date: / / 2023

Week Number:

Student Name: Abdullah refat

ID: 195267

Window types		
name	width	Material
W1	0.5 M	Aluminum frame ,Hooper
W2	1.0 M	Aluminum frame ,sliding
W3	2.0 M	Aluminum frame ,sliding
W4	0.5 M	Aluminum frame ,Awning

Door types		
name	width	Material
D1	1.00 M	Wooden acoustic door,1leaf
D2	0.80 M	Wooden acoustic door,1leaf
D3	0.80 M	Wooden acoustic door,1leaf
D4	2.00 M	Aluminum Sliding door,2leaf

Finishing materials		
Type	No.	Description
Ceiling	1	Plaster Gypsum
	2	False ceiling tiles
	3	Paint
Walls	1	Fiberglass board 25mm,(1")thick
	2	Ceramic tiles 60x60x0.8cm
	3	Paint
	4	Wood panels,tounge and grove decking
Skirting	1	wooden skirting
	2	Ceramic tiles 60x60x0.8cm
	3	Marble skirting
	4	Paint
Flooring	1	Paint
	2	Carpet
	3	Ceramic tiles 60x60x0.8cm
	4	Vinyl tiles

A-14